

PURPOSE:
ADVANCE COPY

COPYRIGHT:
THIS DRAWING IS A COPYRIGHT AND MUST NOT BE DISCLOSED, USED OR REPRODUCED IN ANY FORM WITHOUT THE EXPRESS PERMISSION FROM DISHA VISION.

- GENERAL NOTES:
- DO NOT SCALE THIS DRAWING.
 - ALL THE WRITTEN DIMENSIONS TO BE FOLLOWED.
 - ALL DIMENSIONS ARE IN MM UNLESS OTHERWISE SPECIFIED.
 - ALL THE DIMENSIONS ARE UNFINISHED UNLESS OTHERWISE SPECIFIED.
 - THE SIZES MENTIONED IN SCHEDULE FOR DOORS, WINDOWS & OPENINGS ARE CLEAR MASONRY OPENING SIZES.
 - ANY DISCREPANCY FOUND IN THIS DRAWING SHOULD BE BROUGHT TO THE NOTICE OF THE ARCHITECT BEFORE THE EXECUTION OF WORK.
 - THIS DRAWINGS SHALL BE REFERRED WITH DETAILS, STRUCTURAL, SERVICES AND OTHER RELEVANT DRAWINGS.
 - "DISHA VISION" SHALL NOT BE RESPONSIBLE IN ANY MANNER FOR THE CENTERING, SHUTTERING AND SCAFFOLDING ERECTED AT SITE FOR STRUCTURAL PURPOSE.
 - ALL THE LEVELS SPECIFIED ARE SFL (STRUCTURAL FINISH LEVEL) UNLESS OTHERWISE SPECIFIED.
 - ANY ADDITIONAL EXCAVATION / PROVISION REQUIRED FOR THE PURPOSE OF SOLING, WATERPROOFING, COMPACTION, RAFT SHALL BE AS PER THE DRAWING AND DETAILS GIVEN BY THE STRUCTURAL CONSULTANT & WATERPROOFING AGENCIES.

SCHEDULE FOR OPENINGS:

CONSULTANTS:
STRUCTURAL: POPLI NAGPUR
ELECTRICAL: JHAVERI ASSOCIATES, AHMEDABAD
PLUMBING: JHAVERI ASSOCIATES, AHMEDABAD
FIRE FIGHTING: JHAVERI ASSOCIATES, AHMEDABAD
HVAC: ---
LANDSCAPE: ---

MASONRY DETAILS:
230/200 MM THICK WALL
150 MM THICK WALL
100 MM THICK WALL
LOW HEIGHT WALL

R8	---
R7	---
R6	---
R5	---
R4	---
R3	---
R2	---
R1	05-10-24 Brick work layout & door window schedule
R0	09-11-23 1st draft for structural co-ordination at site
REVISIONS:	

PROJECT:
KARAN KOTHARI BUSINESS PARK

TITLE:
PLOT 1 - GROUND FLOOR PLAN

SCALE:	1:175	NORTH: 
DATE:		
DRAWN BY:		
CHECKED BY:	Akash M.	
DRAWING NO.:	---	

AKASH MOHOTA
+91 7276094577
akash.dishavision@outlook.com
www.dishavision.com
@dishavision
1st Floor, Monalisa Complex,
Opp. to Rajawadi Police Station,
Amravati - 444601

DISHA
VISION
INNOVATE. DESIGN. BUILD


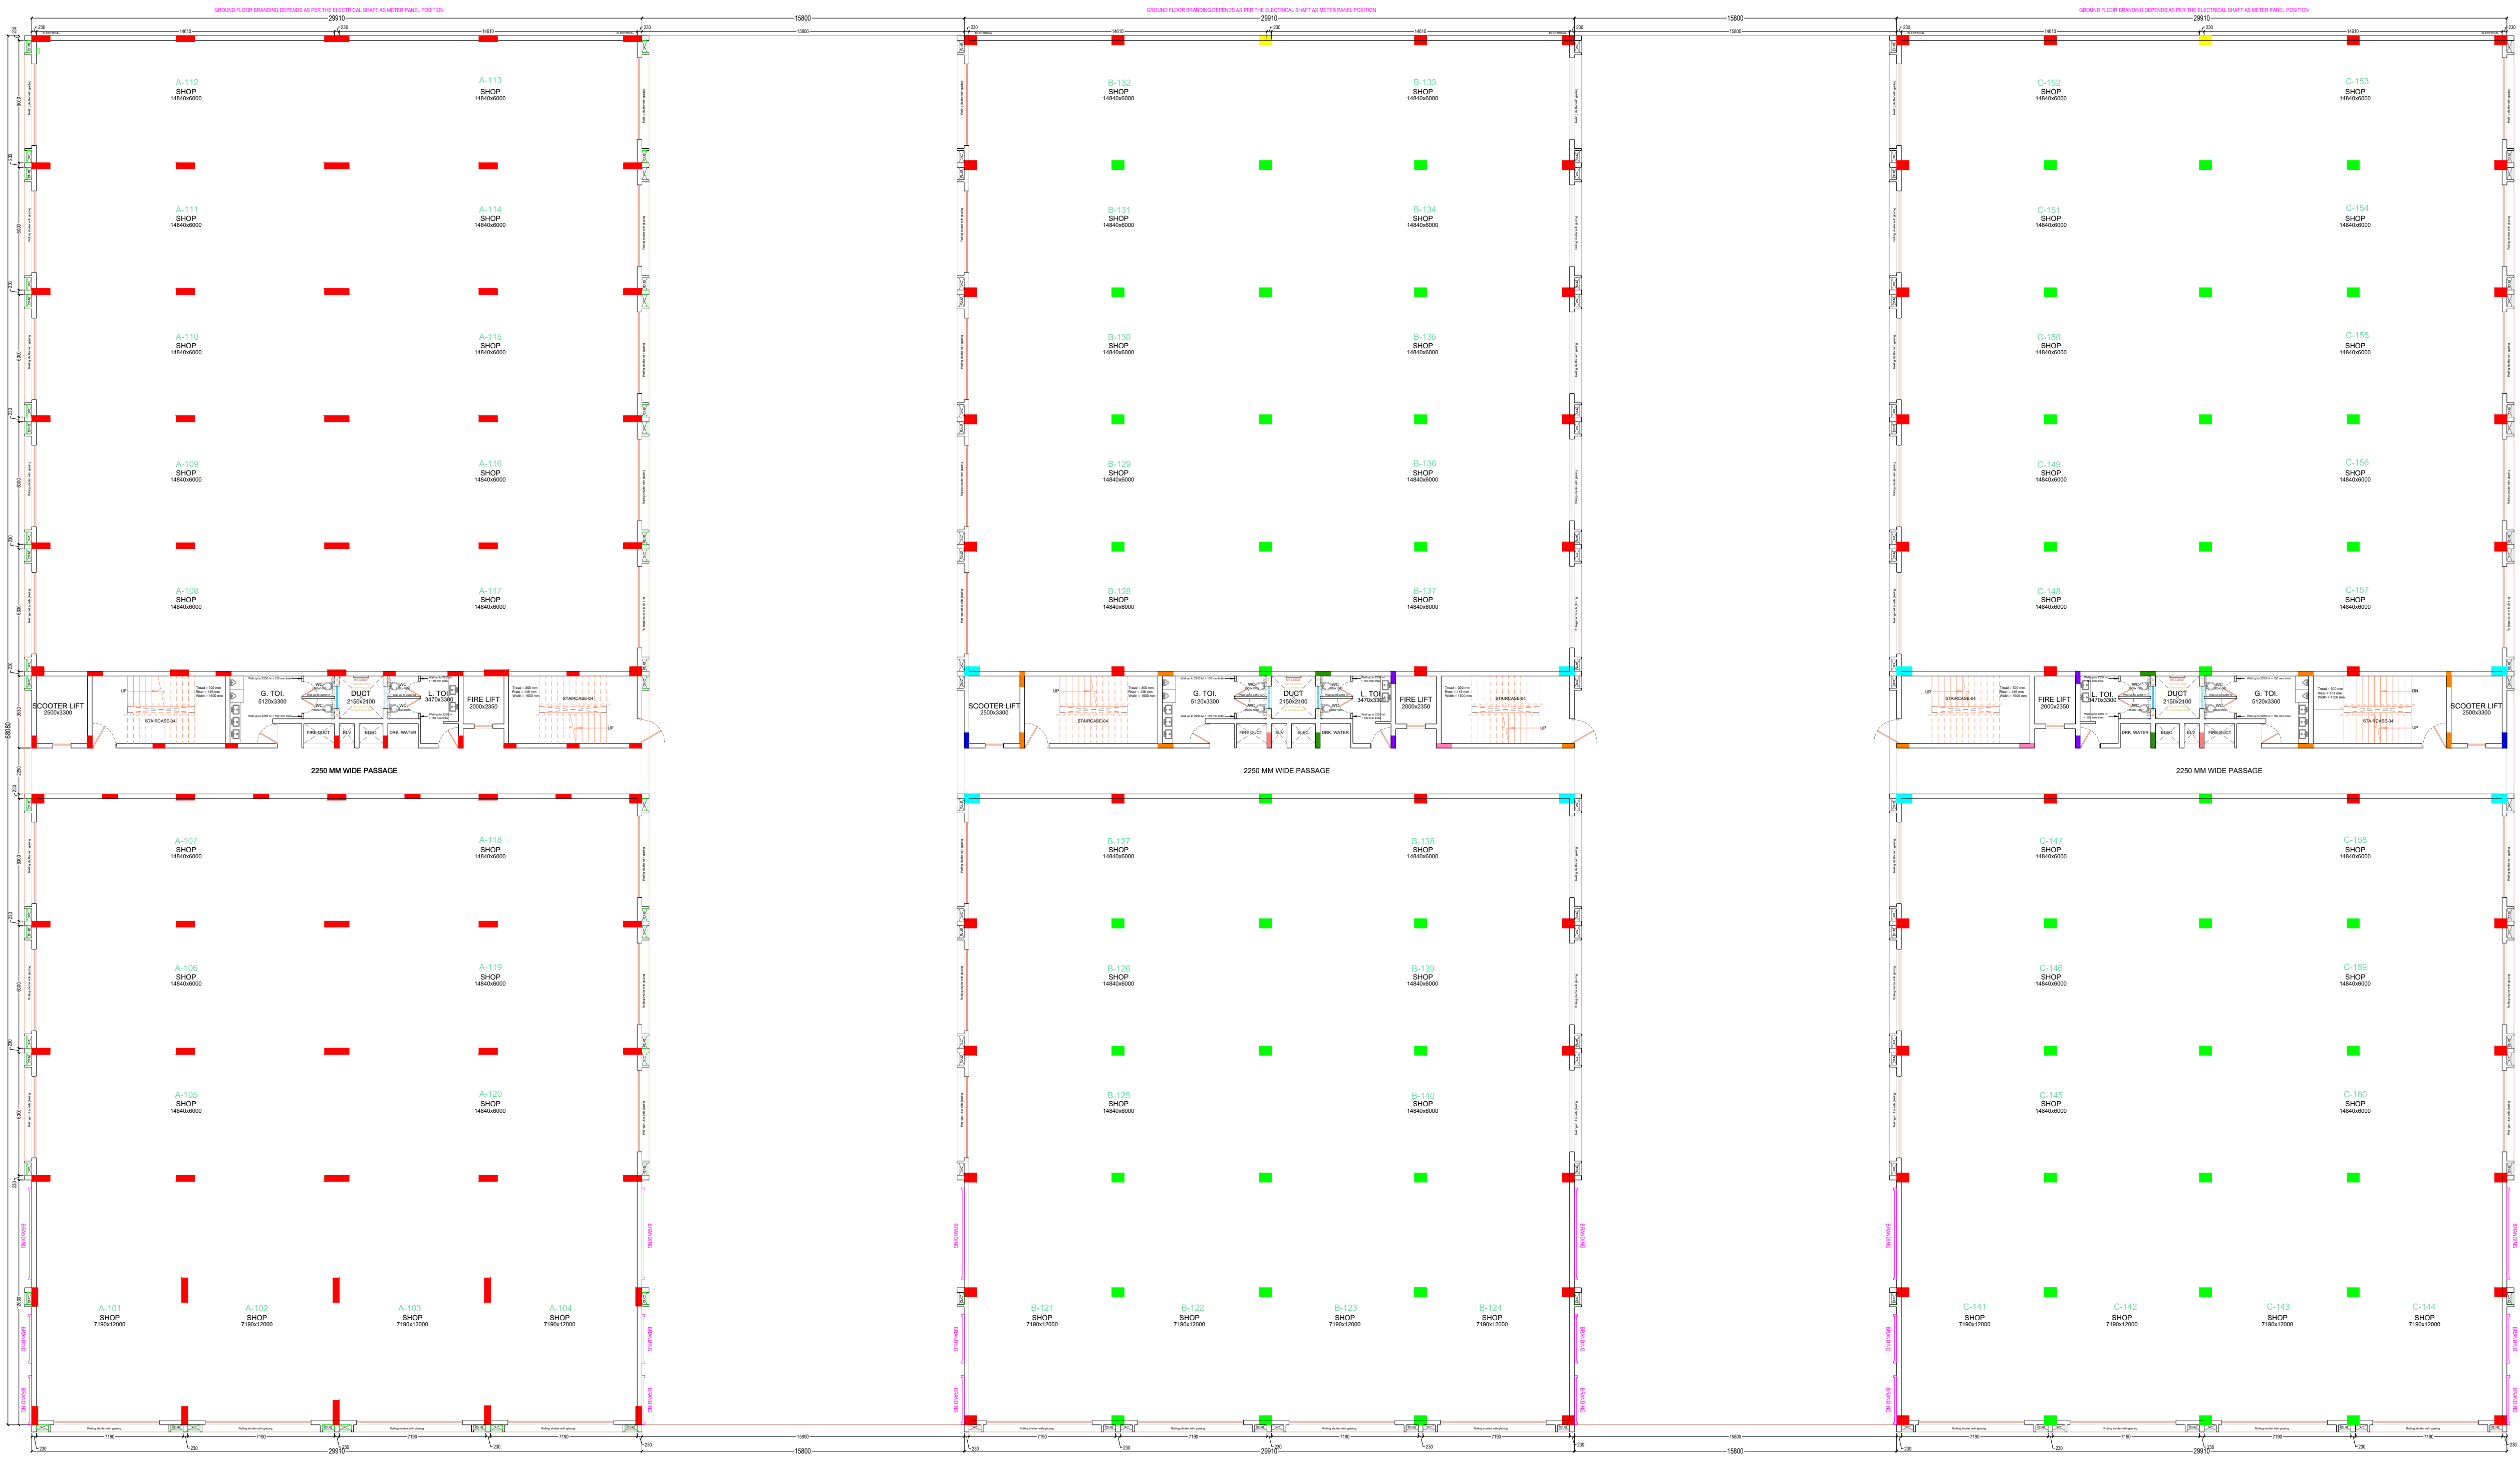


PLATE AREA
GROUND & FIRST FLOOR = 2036.27 SQ.M. / 21918.41 SQ.FT. EACH
SECOND & THIRD FLOOR = 2444.23 SQ.M. / 26309.69 SQ.FT. EACH


GROUND FLOOR WING A

GROUND FLOOR WING B


GROUND FLOOR WING C

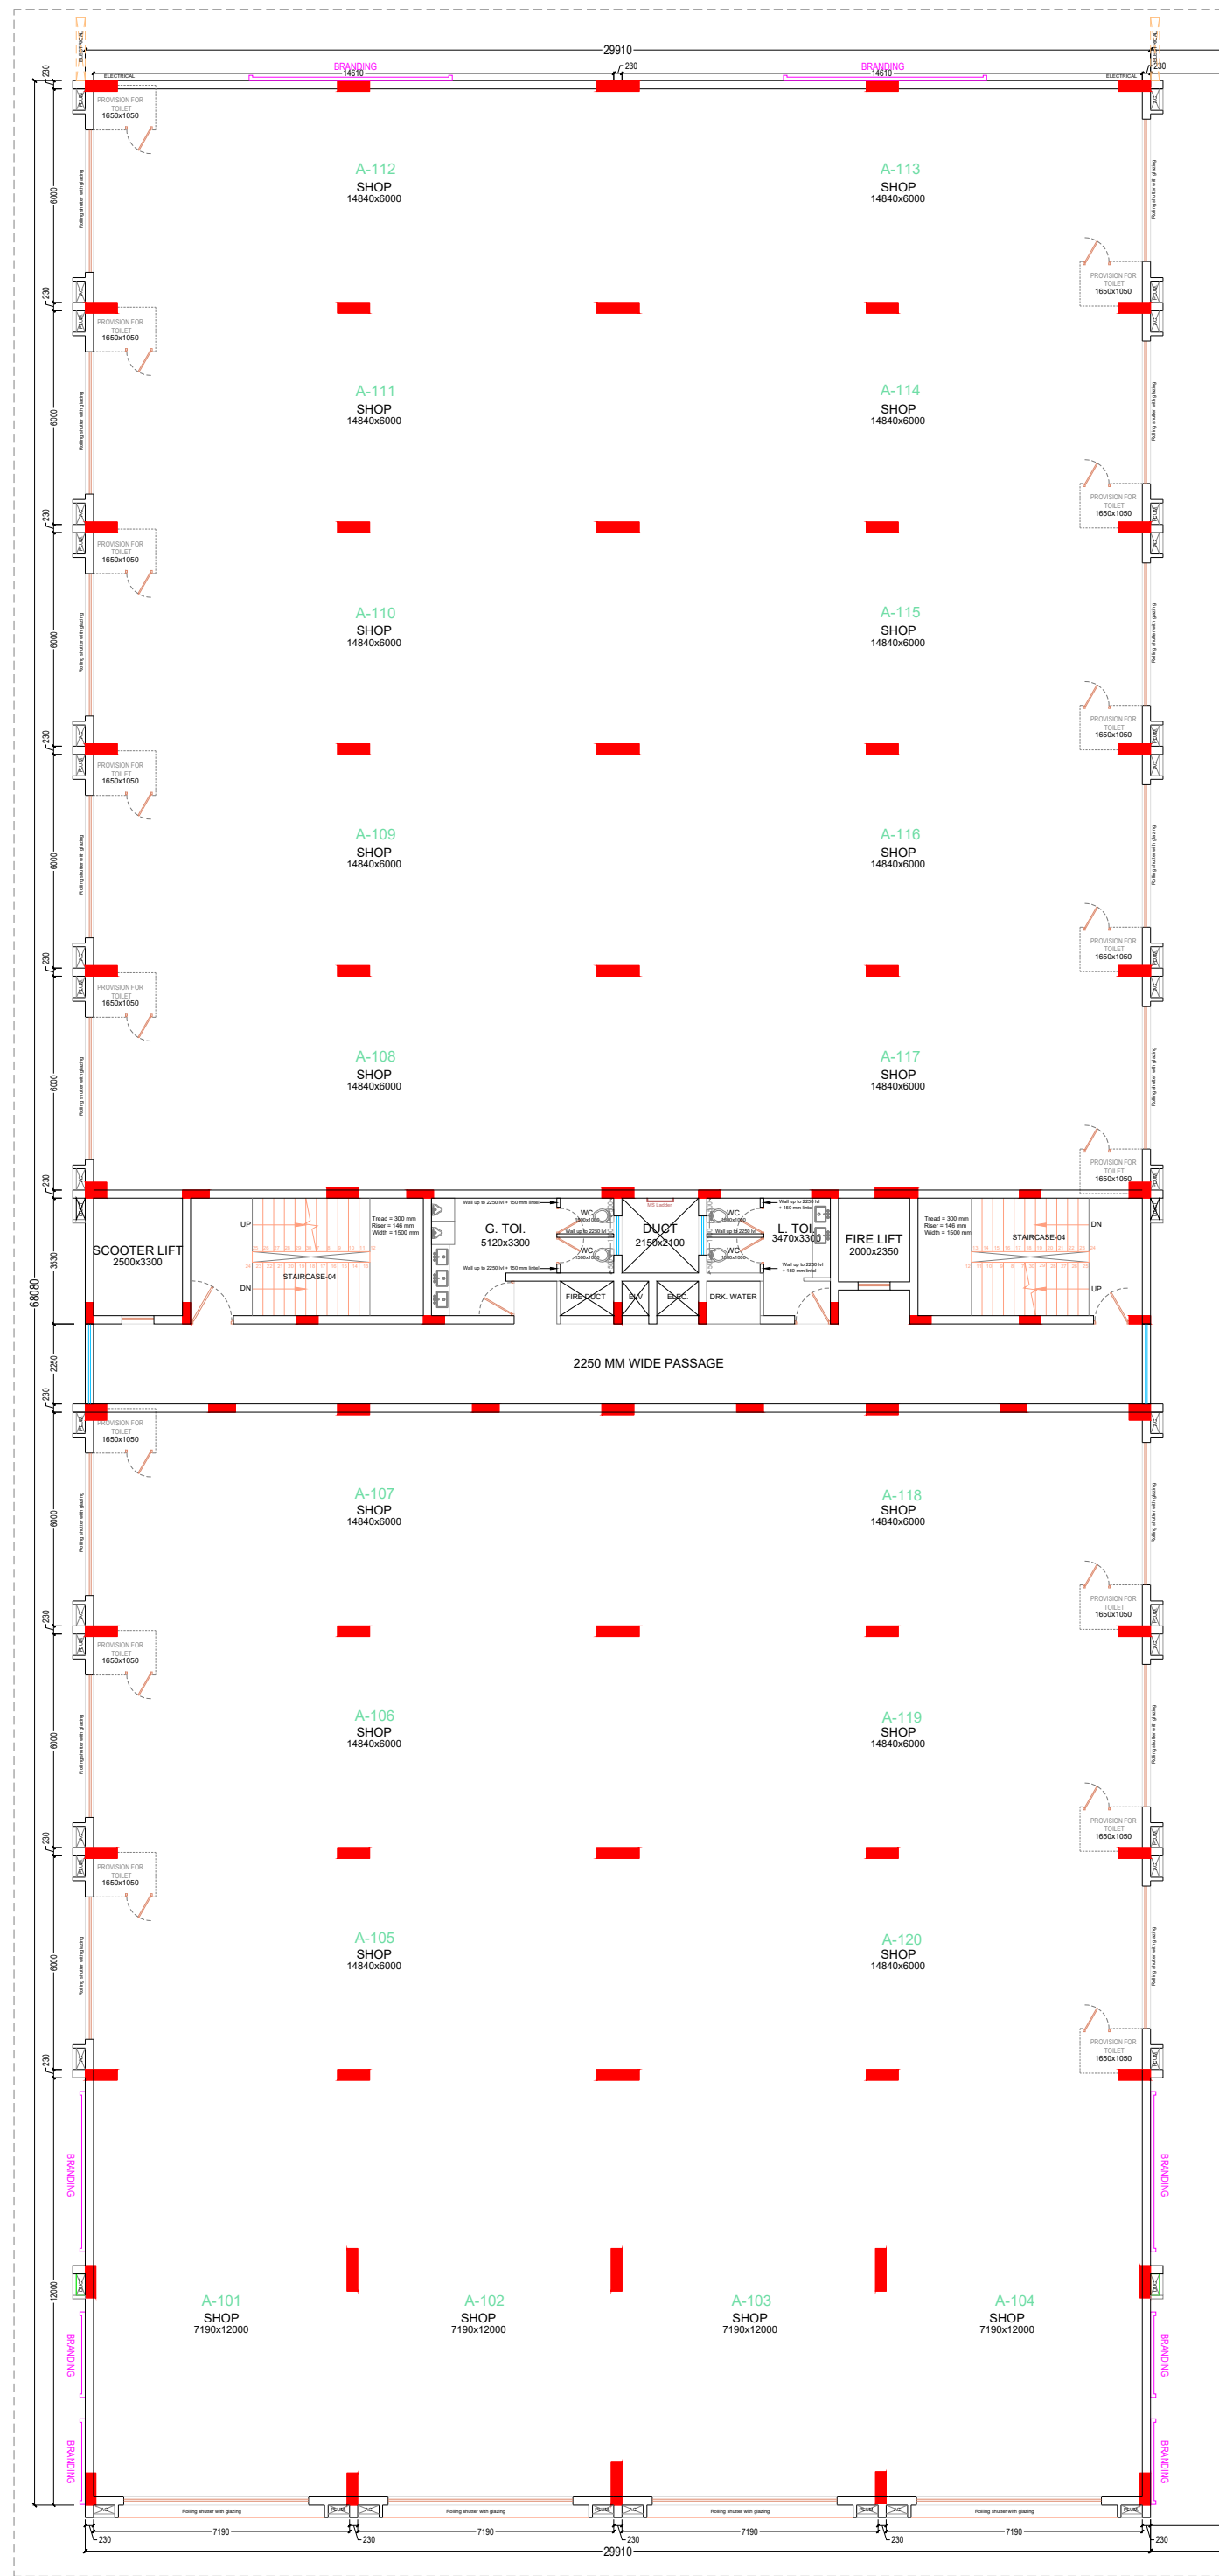

FIRST FLOOR
WING A

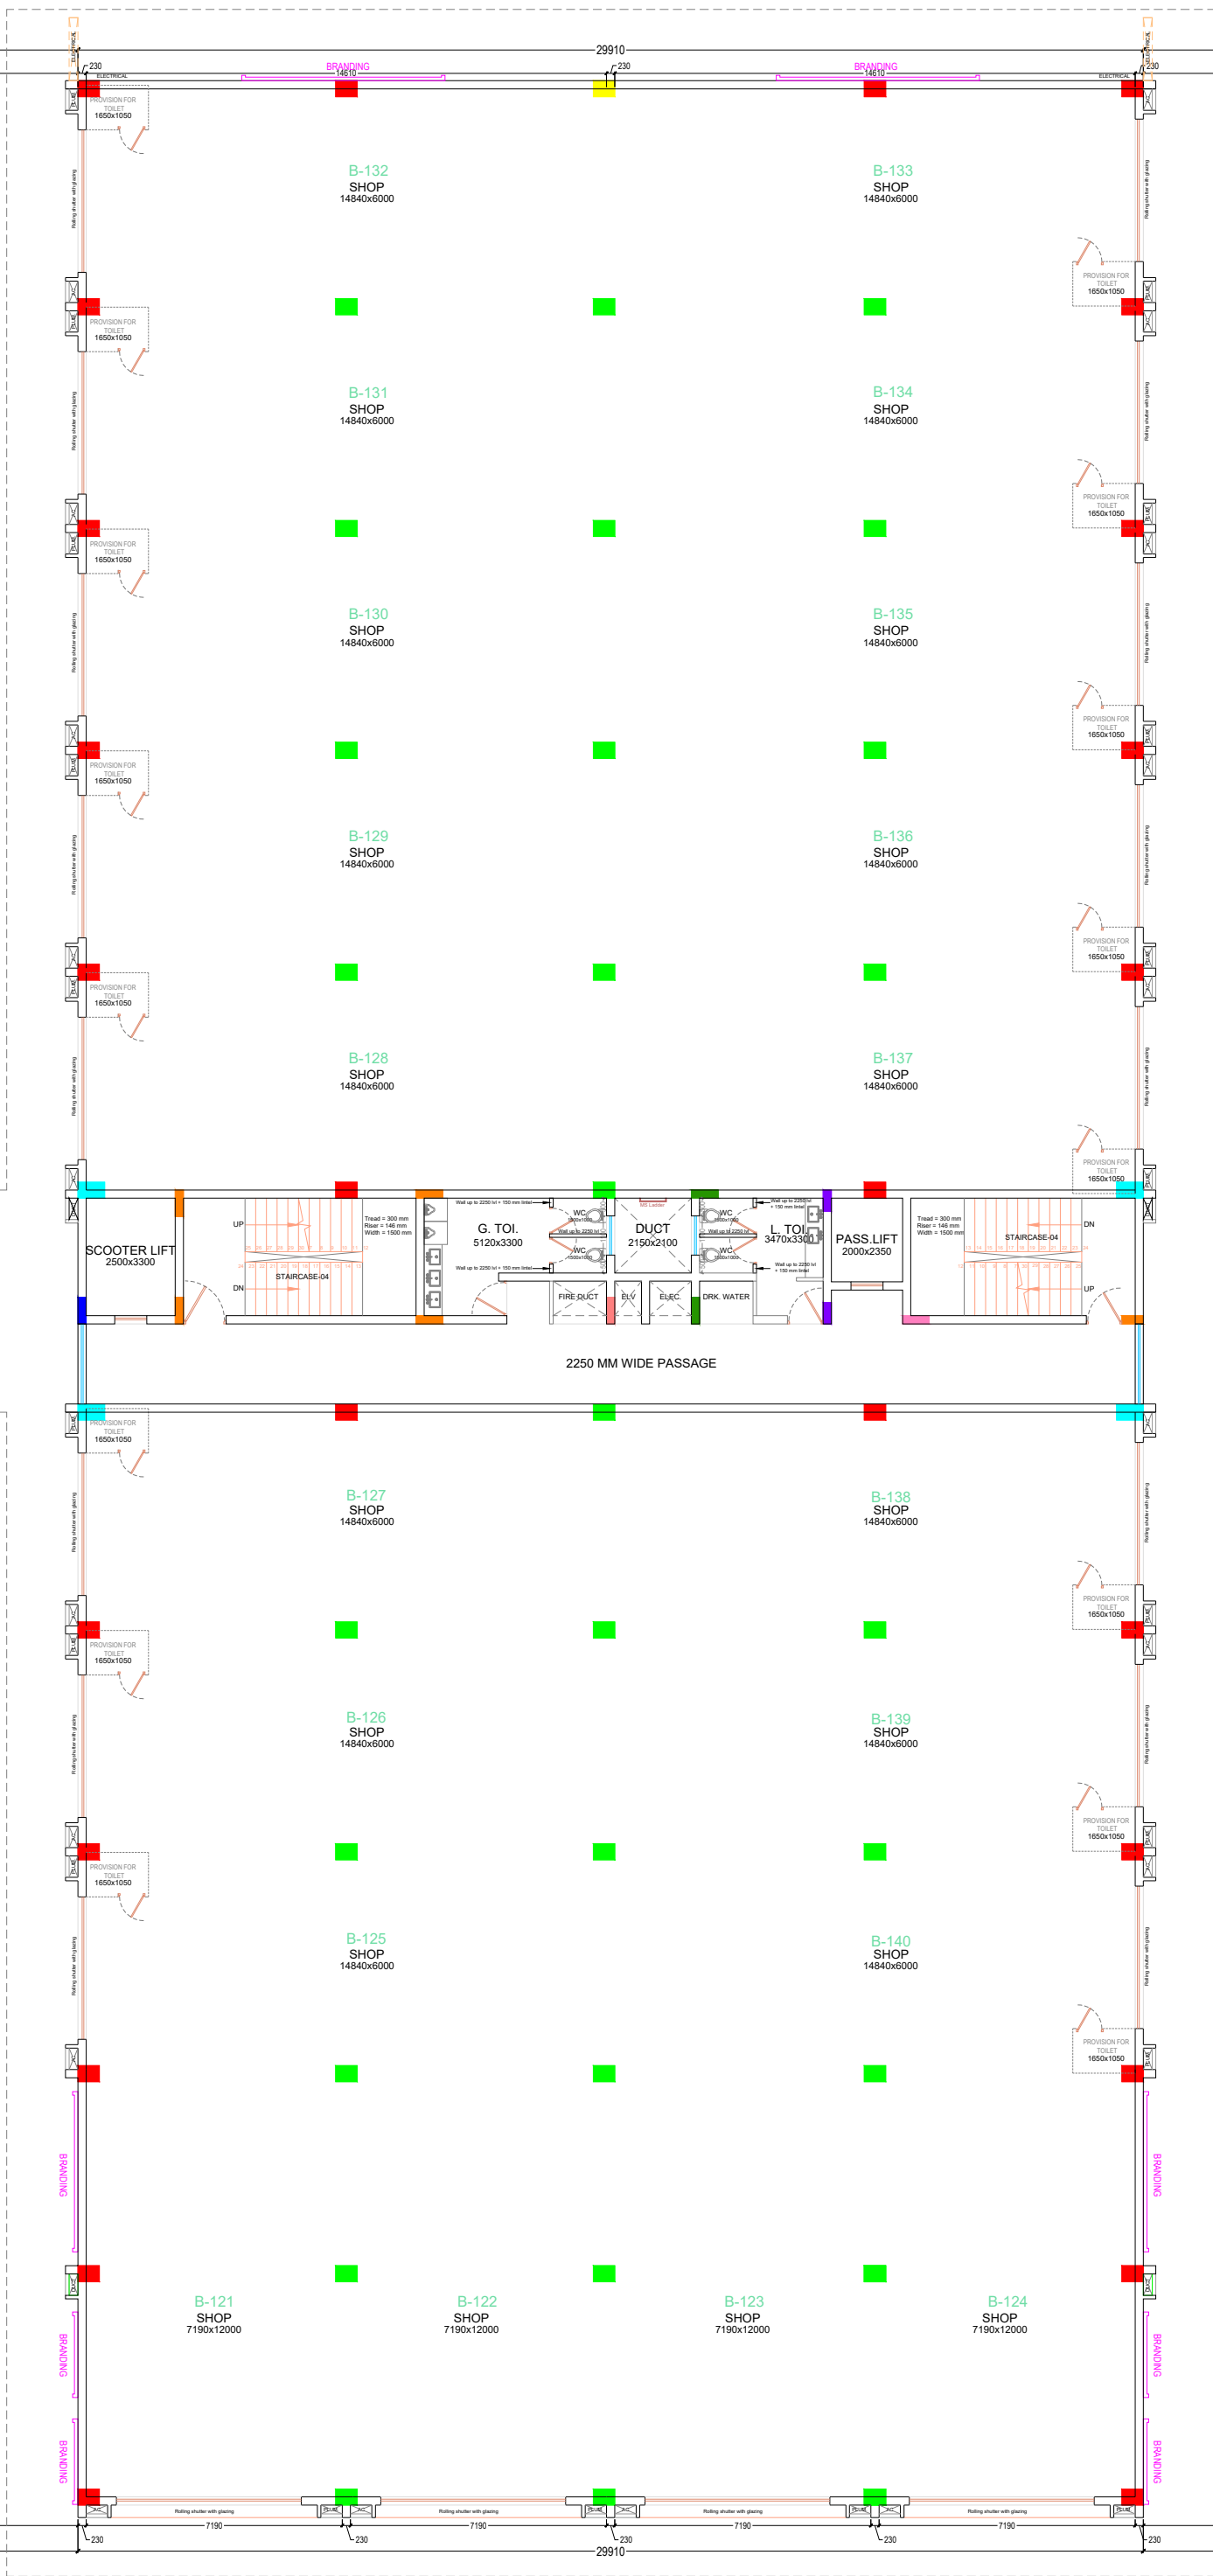

FIRST FLOOR
WING B

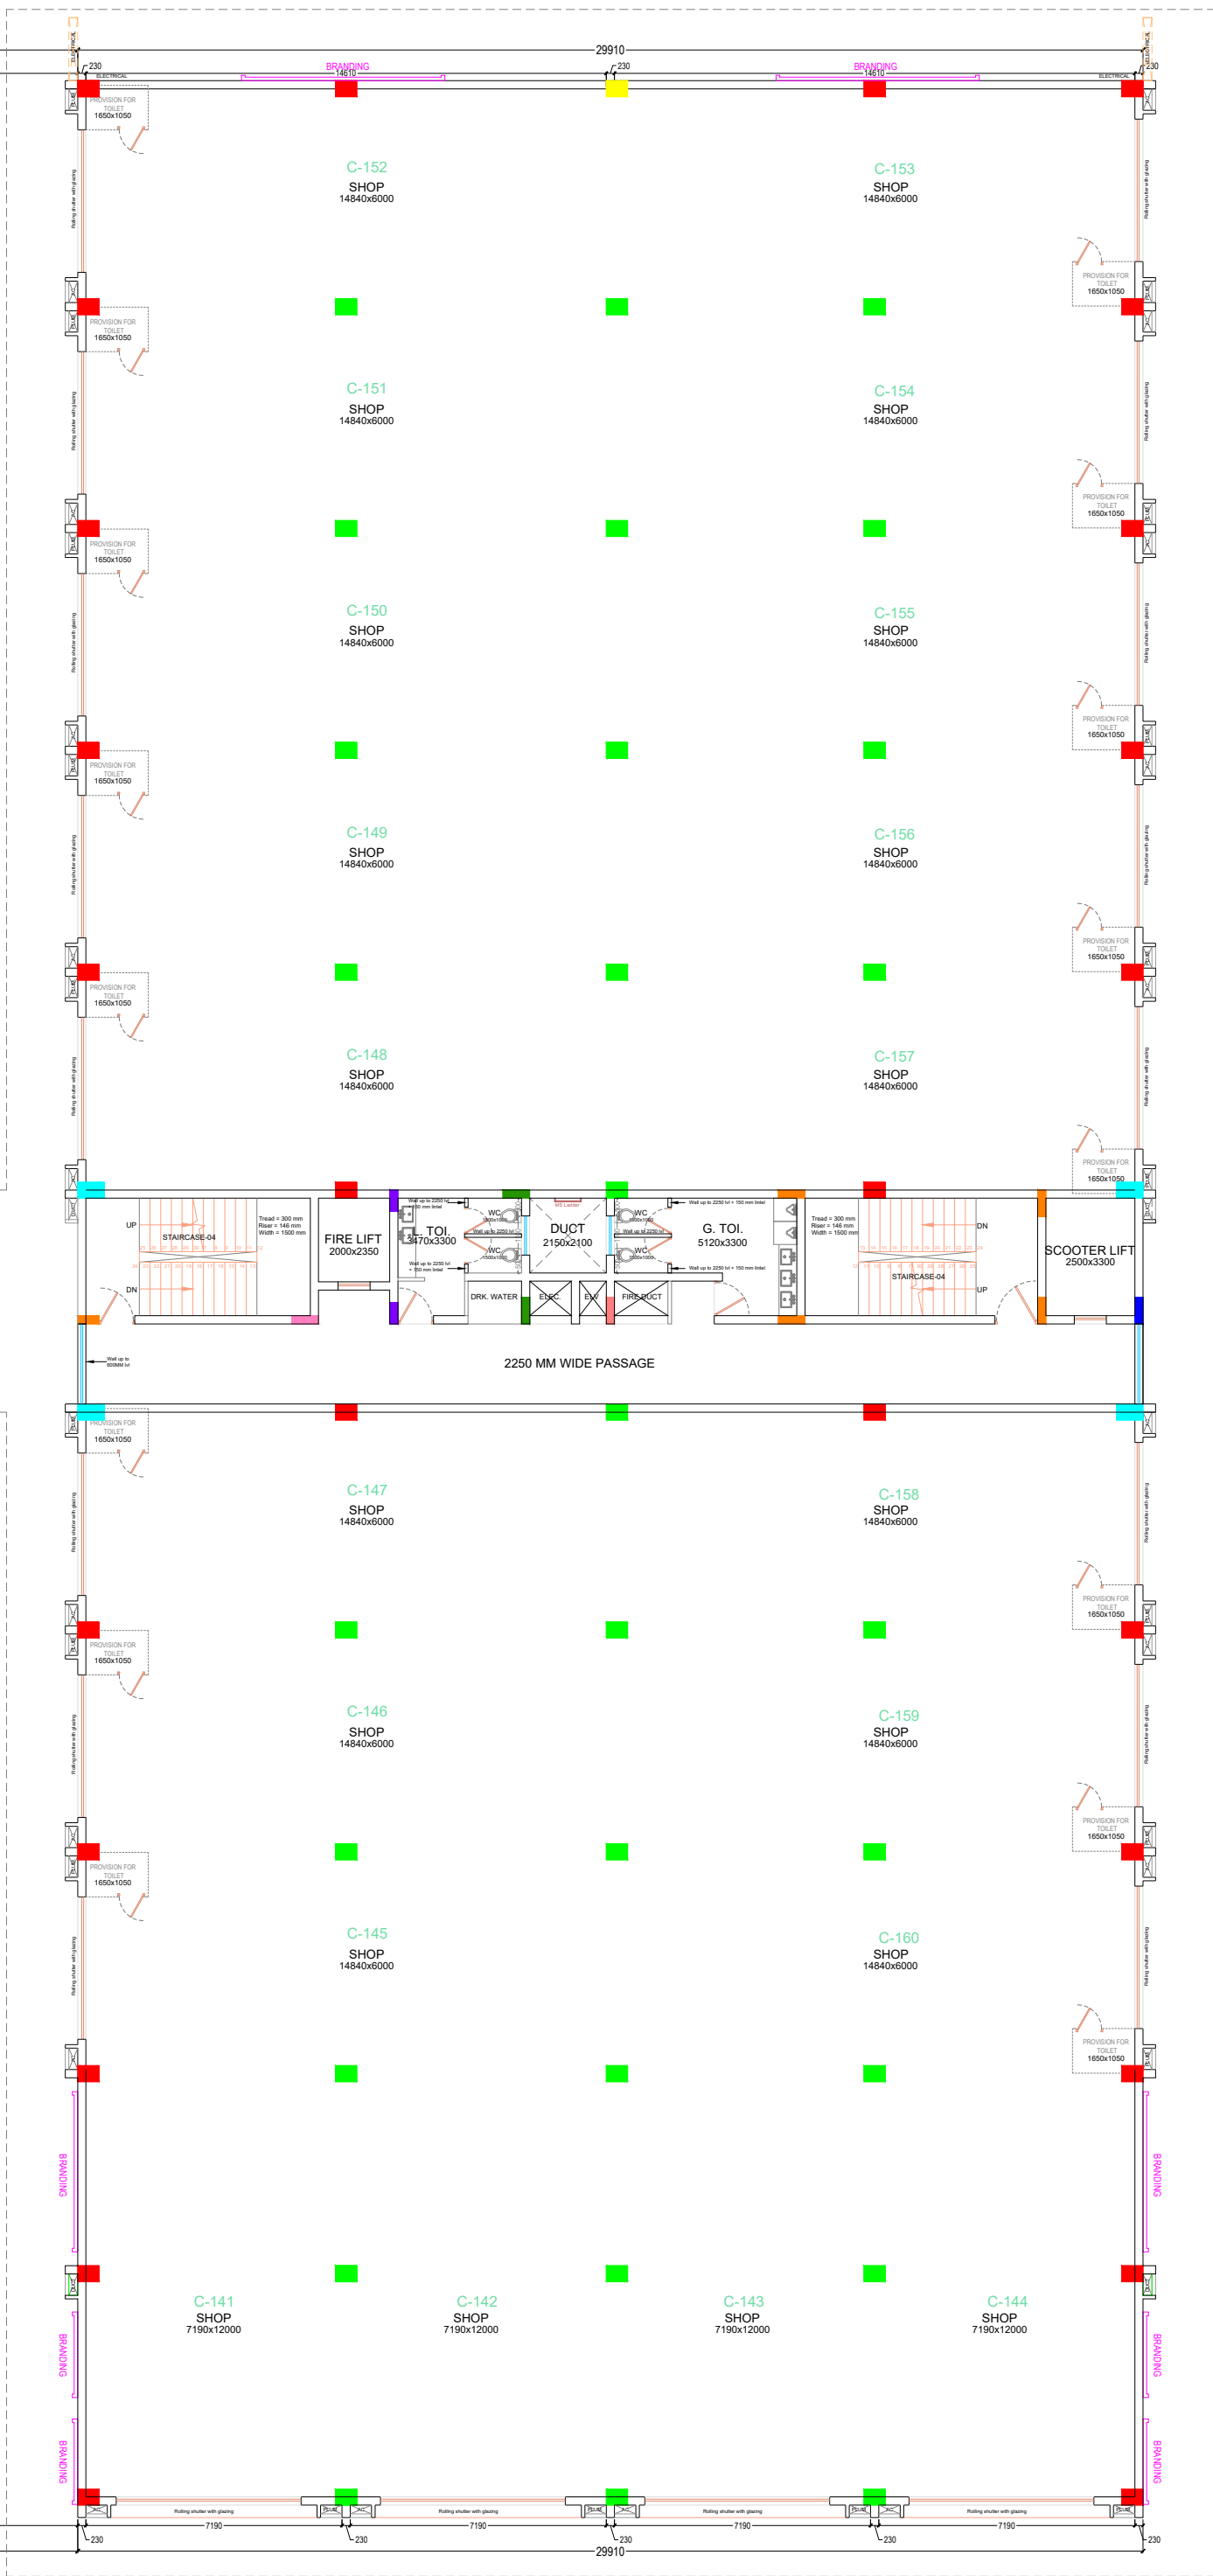

FIRST FLOOR
WING C

STAGE:
WORKING DRAWING

SHEET:
A1

PURPOSE:
ADVANCE COPY

COPYRIGHT:
THIS DRAWING IS A COPYRIGHT AND MUST NOT BE DISCLOSED, USED OR
REPRODUCED IN ANY FORM WITHOUT THE EXPRESS PERMISSION FROM
DISHA VISION.

GENERAL NOTES:
1. DO NOT SCALE THIS DRAWING.
2. ALL THE WRITTEN DIMENSIONS TO BE FOLLOWED.
3. ALL DIMENSIONS ARE IN MM UNLESS OTHERWISE SPECIFIED.
4. ALL THE DIMENSIONS ARE UNFINISHED UNLESS OTHERWISE
SPECIFIED.
5. THE SIZES MENTIONED IN SCHEDULE FOR DOORS, WINDOWS
& OPENINGS ARE CLEAR MASONRY OPENING SIZES.
6. ANY DISCREPANCY FOUND IN THIS DRAWING SHOULD BE
BROUGHT TO THE NOTICE OF THE ARCHITECT BEFORE THE
EXECUTION OF WORK.
7. THIS DRAWINGS SHALL BE REFERRED WITH DETAILS,
STRUCTURAL SERVICES AND OTHER RELEVANT DRAWINGS.
8. "DISHA VISION" SHALL NOT BE RESPONSIBLE IN ANY
MANNER FOR THE CENTERING, SHUTTERING AND
SCAFFOLDING ERECTED AT SITE FOR STRUCTURAL
PURPOSE.
9. ALL THE LEVELS SPECIFIED ARE SFL (STRUCTURAL FINISH
LEVEL) UNLESS OTHERWISE SPECIFIED.
10. ANY ADDITIONAL EXCAVATION / PROVISION REQUIRED FOR
THE PURPOSE OF SOLING, WATERPROOFING, COMPACTION,
RAFT SHALL BE AS PER THE DRAWING AND DETAILS GIVEN
BY THE STRUCTURAL CONSULTANT & WATERPROOFING
AGENCIES.

SCHEDULE FOR OPENINGS:

CONSULTANTS:
STRUCTURAL: POPLI NAGPUR
ELECTRICAL: JHAVERI ASSOCIATES, AHMEDABAD
PLUMBING: JHAVERI ASSOCIATES, AHMEDABAD
FIRE FIGHTING: JHAVERI ASSOCIATES, AHMEDABAD
HVAC: ---
LANDSCAPE: ---

MASONRY DETAILS:
230/200 MM THICK WALL
150 MM THICK WALL
100 MM THICK WALL
LOW HEIGHT WALL


R8	---
R7	---
R6	---
R5	---
R4	---
R3	---
R2	---
R1	05-10-24 Brick work layout & door window schedule
R0	09-11-23 1st draft for structural co-ordination at site
REVISIONS:	

PROJECT:
KARAN KOTHARI BUSINESS PARK


TITLE:
PLOT 1 - FIRST FLOOR PLAN

SCALE:	1:175	NORTH:
DATE:		
DRAWN BY:		
CHECKED BY:	Akash M.	
DRAWING NO.:	---	


AKASH MOHOTA
+91 7276094577
akash.dishavision@outlook.com
www.dishavision.com
@dishavision
1st Floor, Monalisa Complex,
Opp. to Rajawadi Police Station,
Amravati - 444601

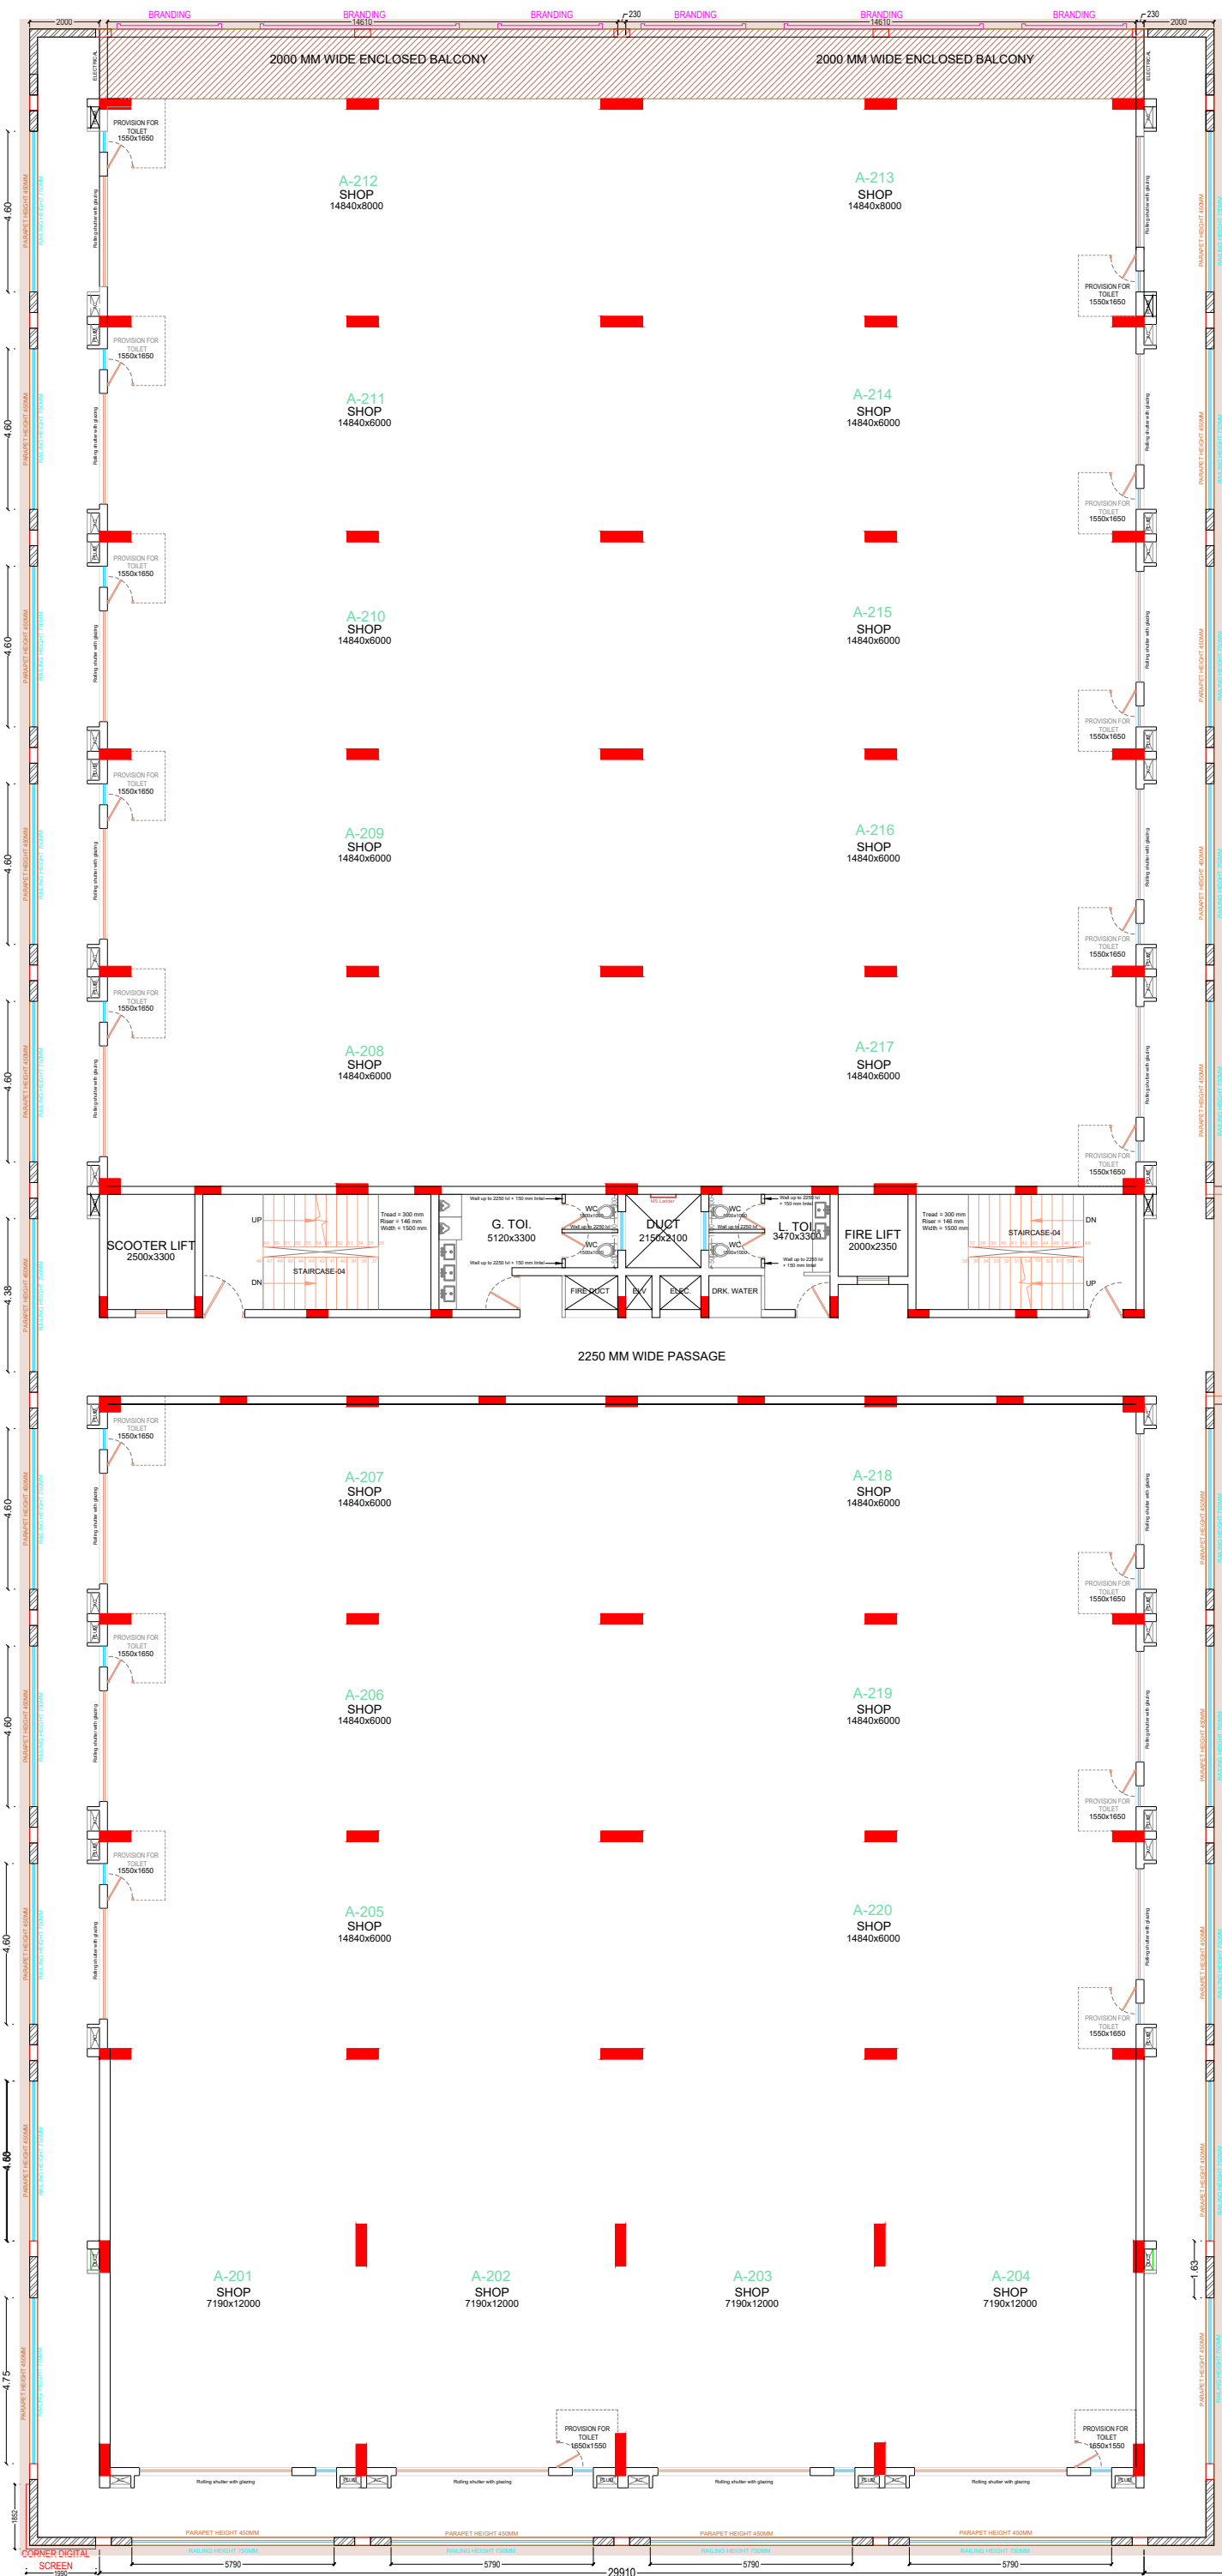

SECOND FLOOR
WING A

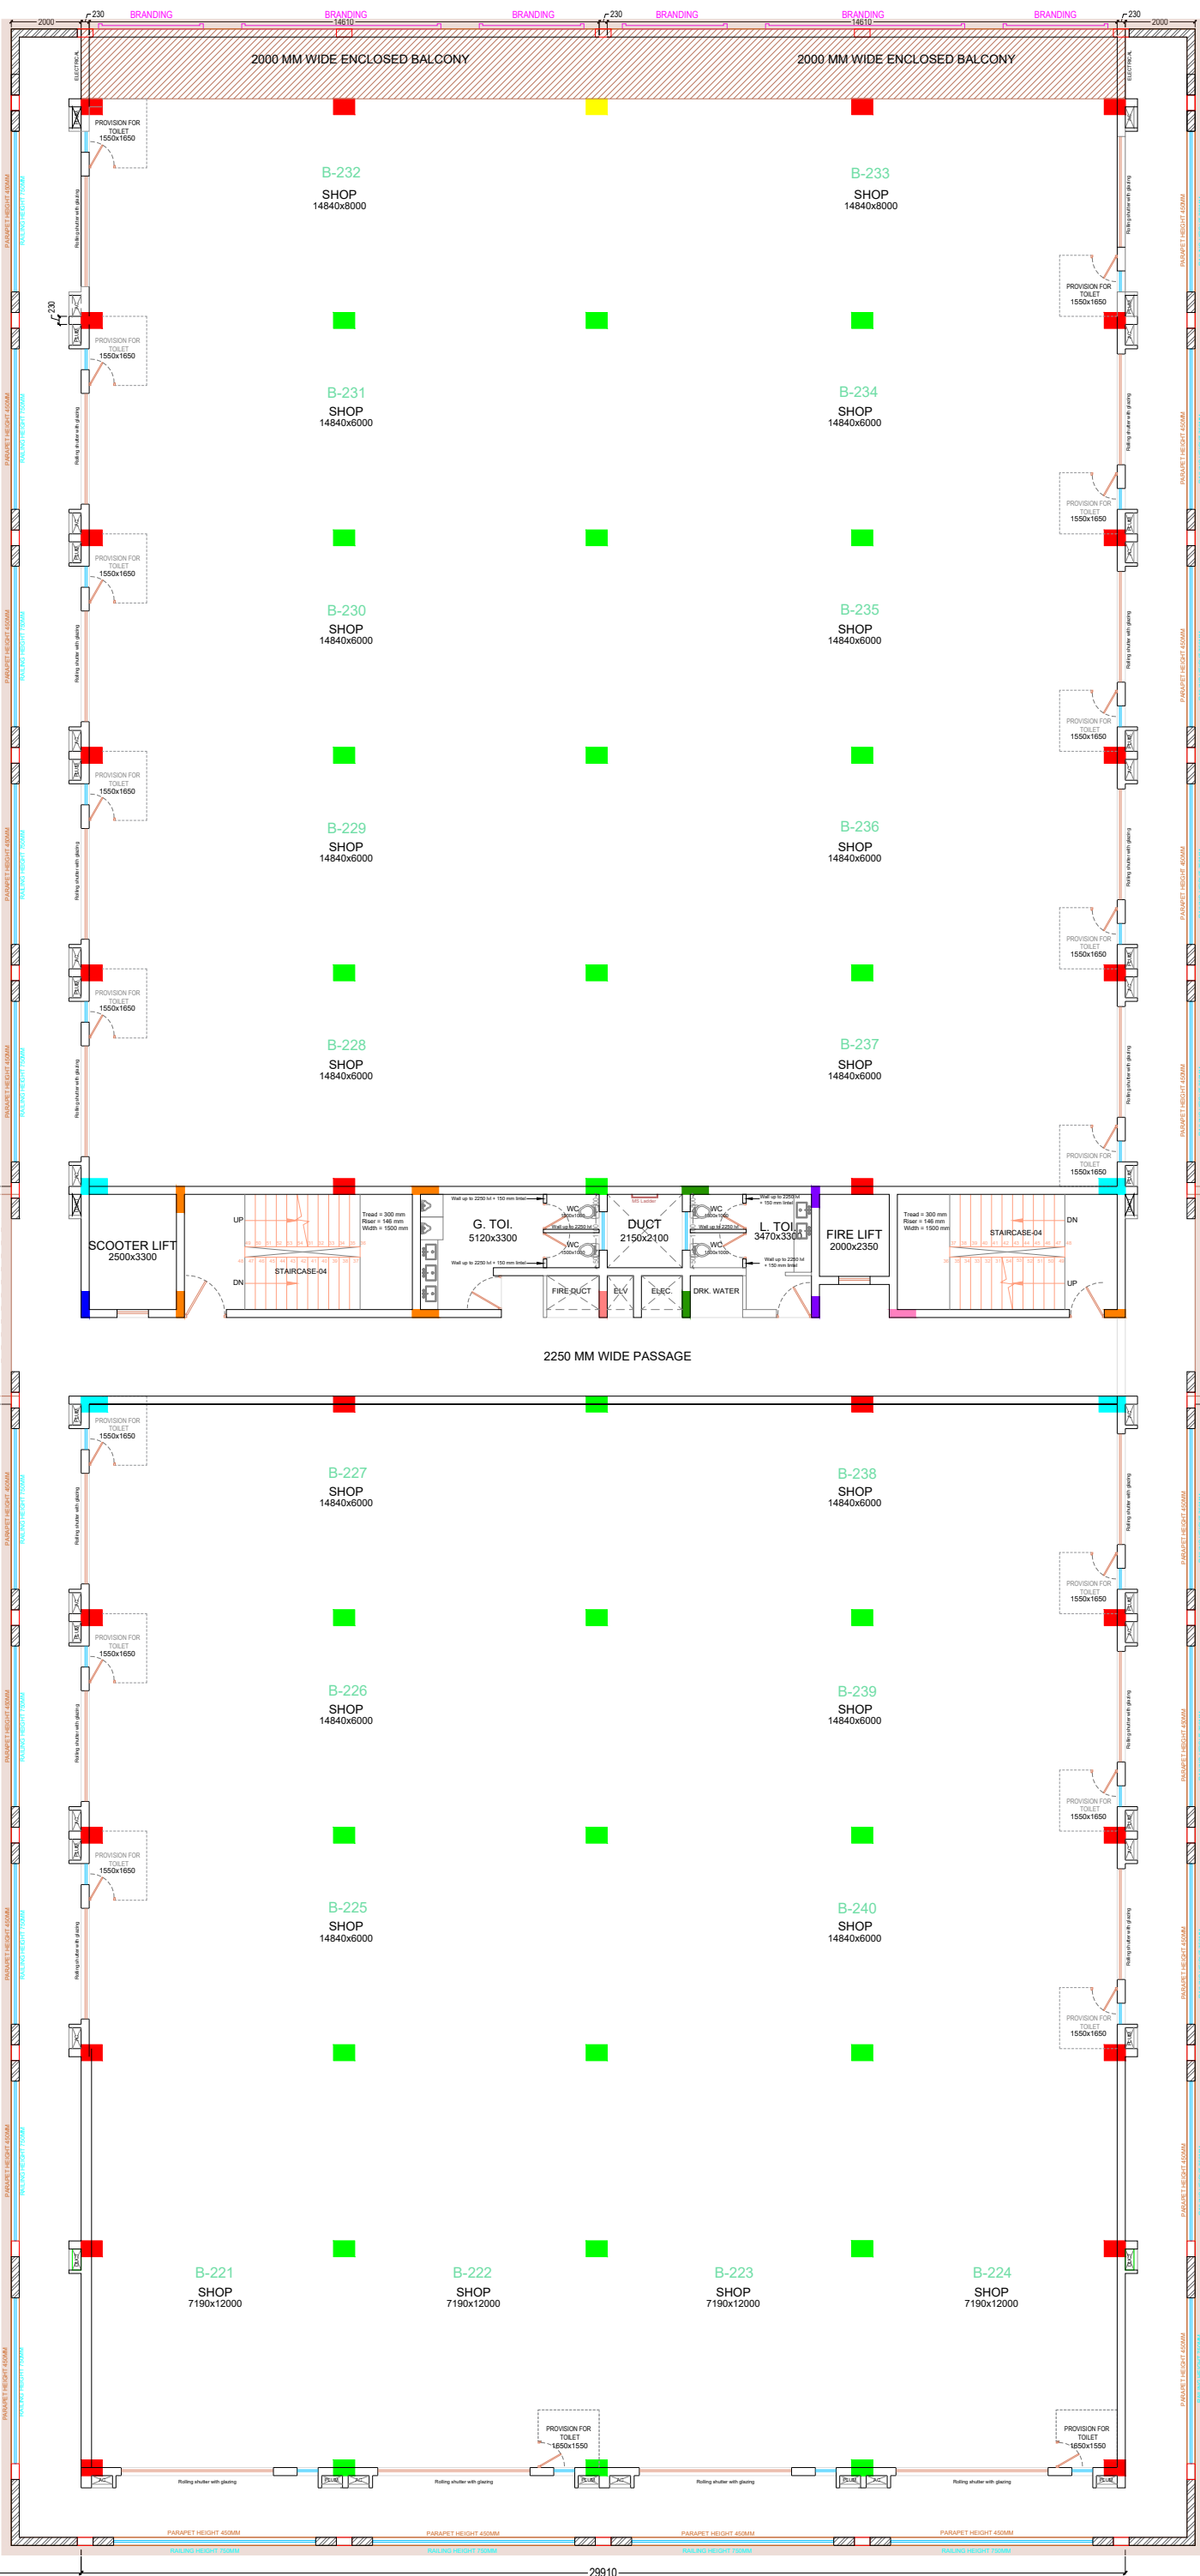

SECOND FLOOR
WING B

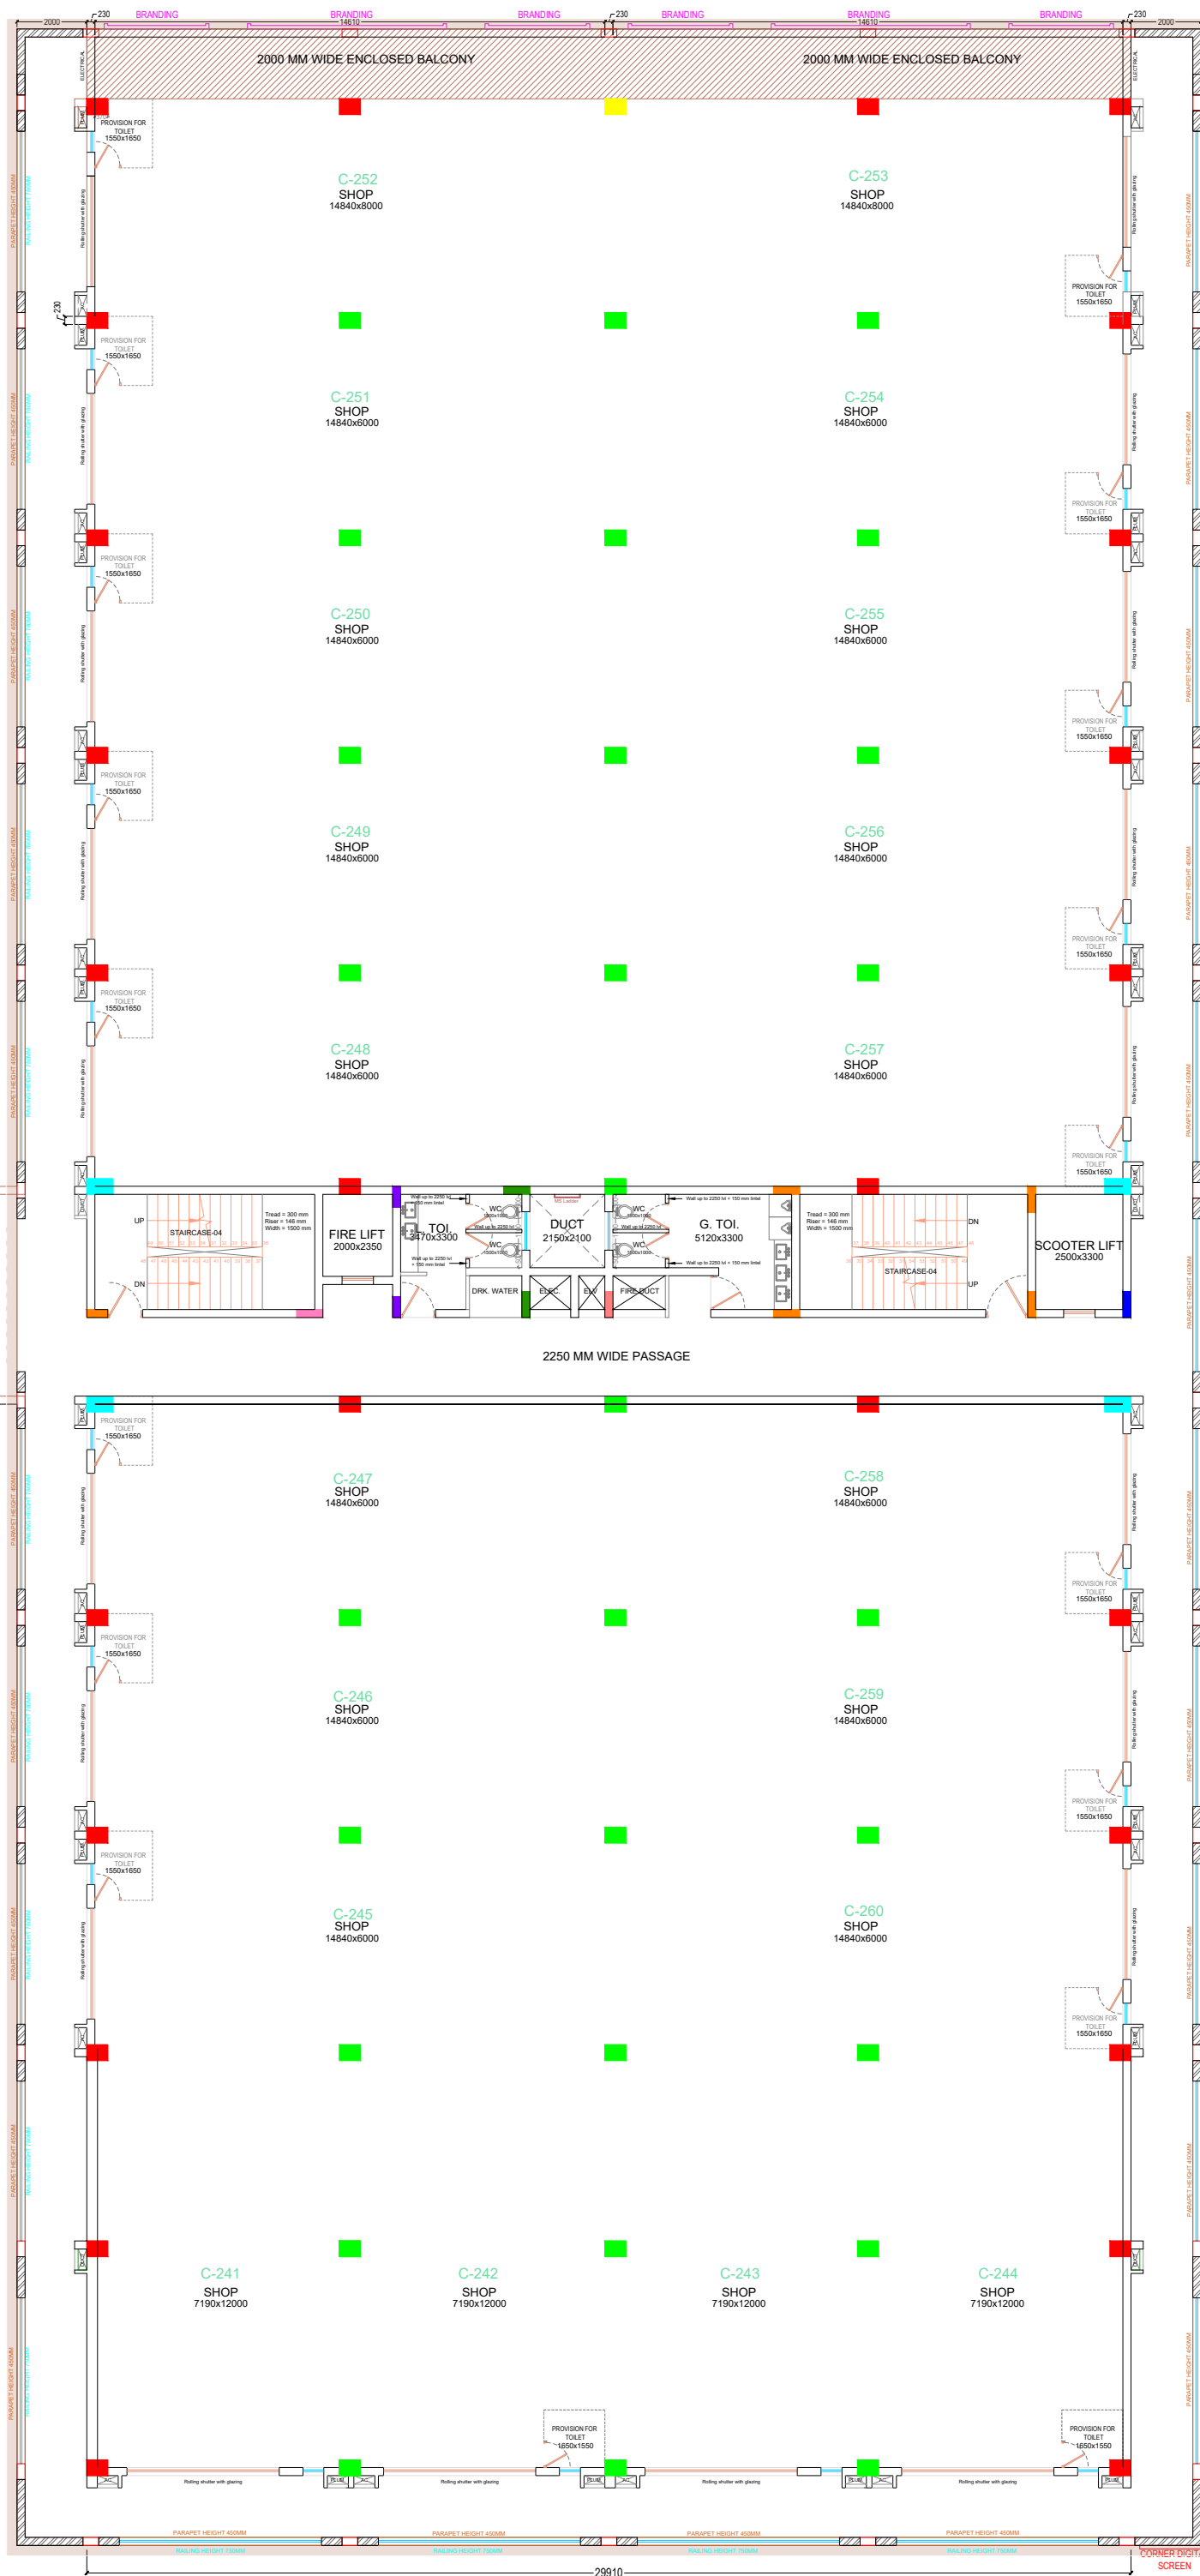

SECOND FLOOR
WING C

STAGE:
WORKING DRAWING

SHEET:
A1

PURPOSE:
ADVANCE COPY

COPYRIGHT:
THIS DRAWING IS A COPYRIGHT AND MUST NOT BE DISCLOSED, USED OR REPRODUCED IN ANY FORM WITHOUT THE EXPRESS PERMISSION FROM DISHA VISION.

- GENERAL NOTES:
- DO NOT SCALE THIS DRAWING.
 - ALL THE WRITTEN DIMENSIONS TO BE FOLLOWED.
 - ALL DIMENSIONS ARE IN MM UNLESS OTHERWISE SPECIFIED.
 - ALL THE DIMENSIONS ARE UNFINISHED UNLESS OTHERWISE SPECIFIED.
 - THE SIZES MENTIONED IN SCHEDULE FOR DOORS, WINDOWS & OPENINGS ARE CLEAR MASONRY OPENING SIZES.
 - ANY DISCREPANCY FOUND IN THIS DRAWING SHOULD BE BROUGHT TO THE NOTICE OF THE ARCHITECT BEFORE THE EXECUTION OF WORK.
 - THIS DRAWINGS SHALL BE REFERRED WITH DETAILS, STRUCTURAL SERVICES AND OTHER RELEVANT DRAWINGS.
 - "DISHA VISION" SHALL NOT BE RESPONSIBLE IN ANY MANNER FOR THE CENTERING, SHUTTERING AND SCAFFOLDING ERECTED AT SITE FOR STRUCTURAL PURPOSE.
 - ALL THE LEVELS SPECIFIED ARE SFL (STRUCTURAL FINISH LEVEL) UNLESS OTHERWISE SPECIFIED.
 - ANY ADDITIONAL EXCAVATION / PROVISION REQUIRED FOR THE PURPOSE OF SOLING, WATERPROOFING, COMPACTION, RAFT SHALL BE AS PER THE DRAWING AND DETAILS GIVEN BY THE STRUCTURAL CONSULTANT & WATERPROOFING AGENCIES.

SCHEDULE FOR OPENINGS:

CONSULTANTS:

STRUCTURAL: PCPL, NAGPUR
ELECTRICAL: JHAVERI ASSOCIATES, AHMEDABAD
PLUMBING: JHAVERI ASSOCIATES, AHMEDABAD
FIRE FIGHTING: JHAVERI ASSOCIATES, AHMEDABAD
HVAC: ---
LANDSCAPE: ---

MASONRY DETAILS:

230/200 MM THICK WALL 150 MM THICK WALL
100 MM THICK WALL LOW HEIGHT WALL

R8	---
R7	---
R6	---
R5	---
R4	---
R3	---
R2	---
R1	05-10-24 Brick work layout & door window schedule
R0	09-11-23 1st draft for structural co-ordination at site
REVISIONS:	


PROJECT:
KARAN KOTHARI BUSINESS PARK

TITLE:
PLOT 1 - SECOND FLOOR PLAN


SCALE:	1:175	NORTH:
DATE:		
DRAWN BY:		
CHECKED BY:	Akash M.	
DRAWING NO.:	---	

AKASH MOHOTA
+91 7276094577
akash.dishavision@outlook.com
www.dishavision.com
@dishavision
1st Floor, Monalisa Complex,
Opp. to Rajawade Police Station,
Amravati - 444601


DISHA
VISION
INNOVATE. DESIGN. BUILD

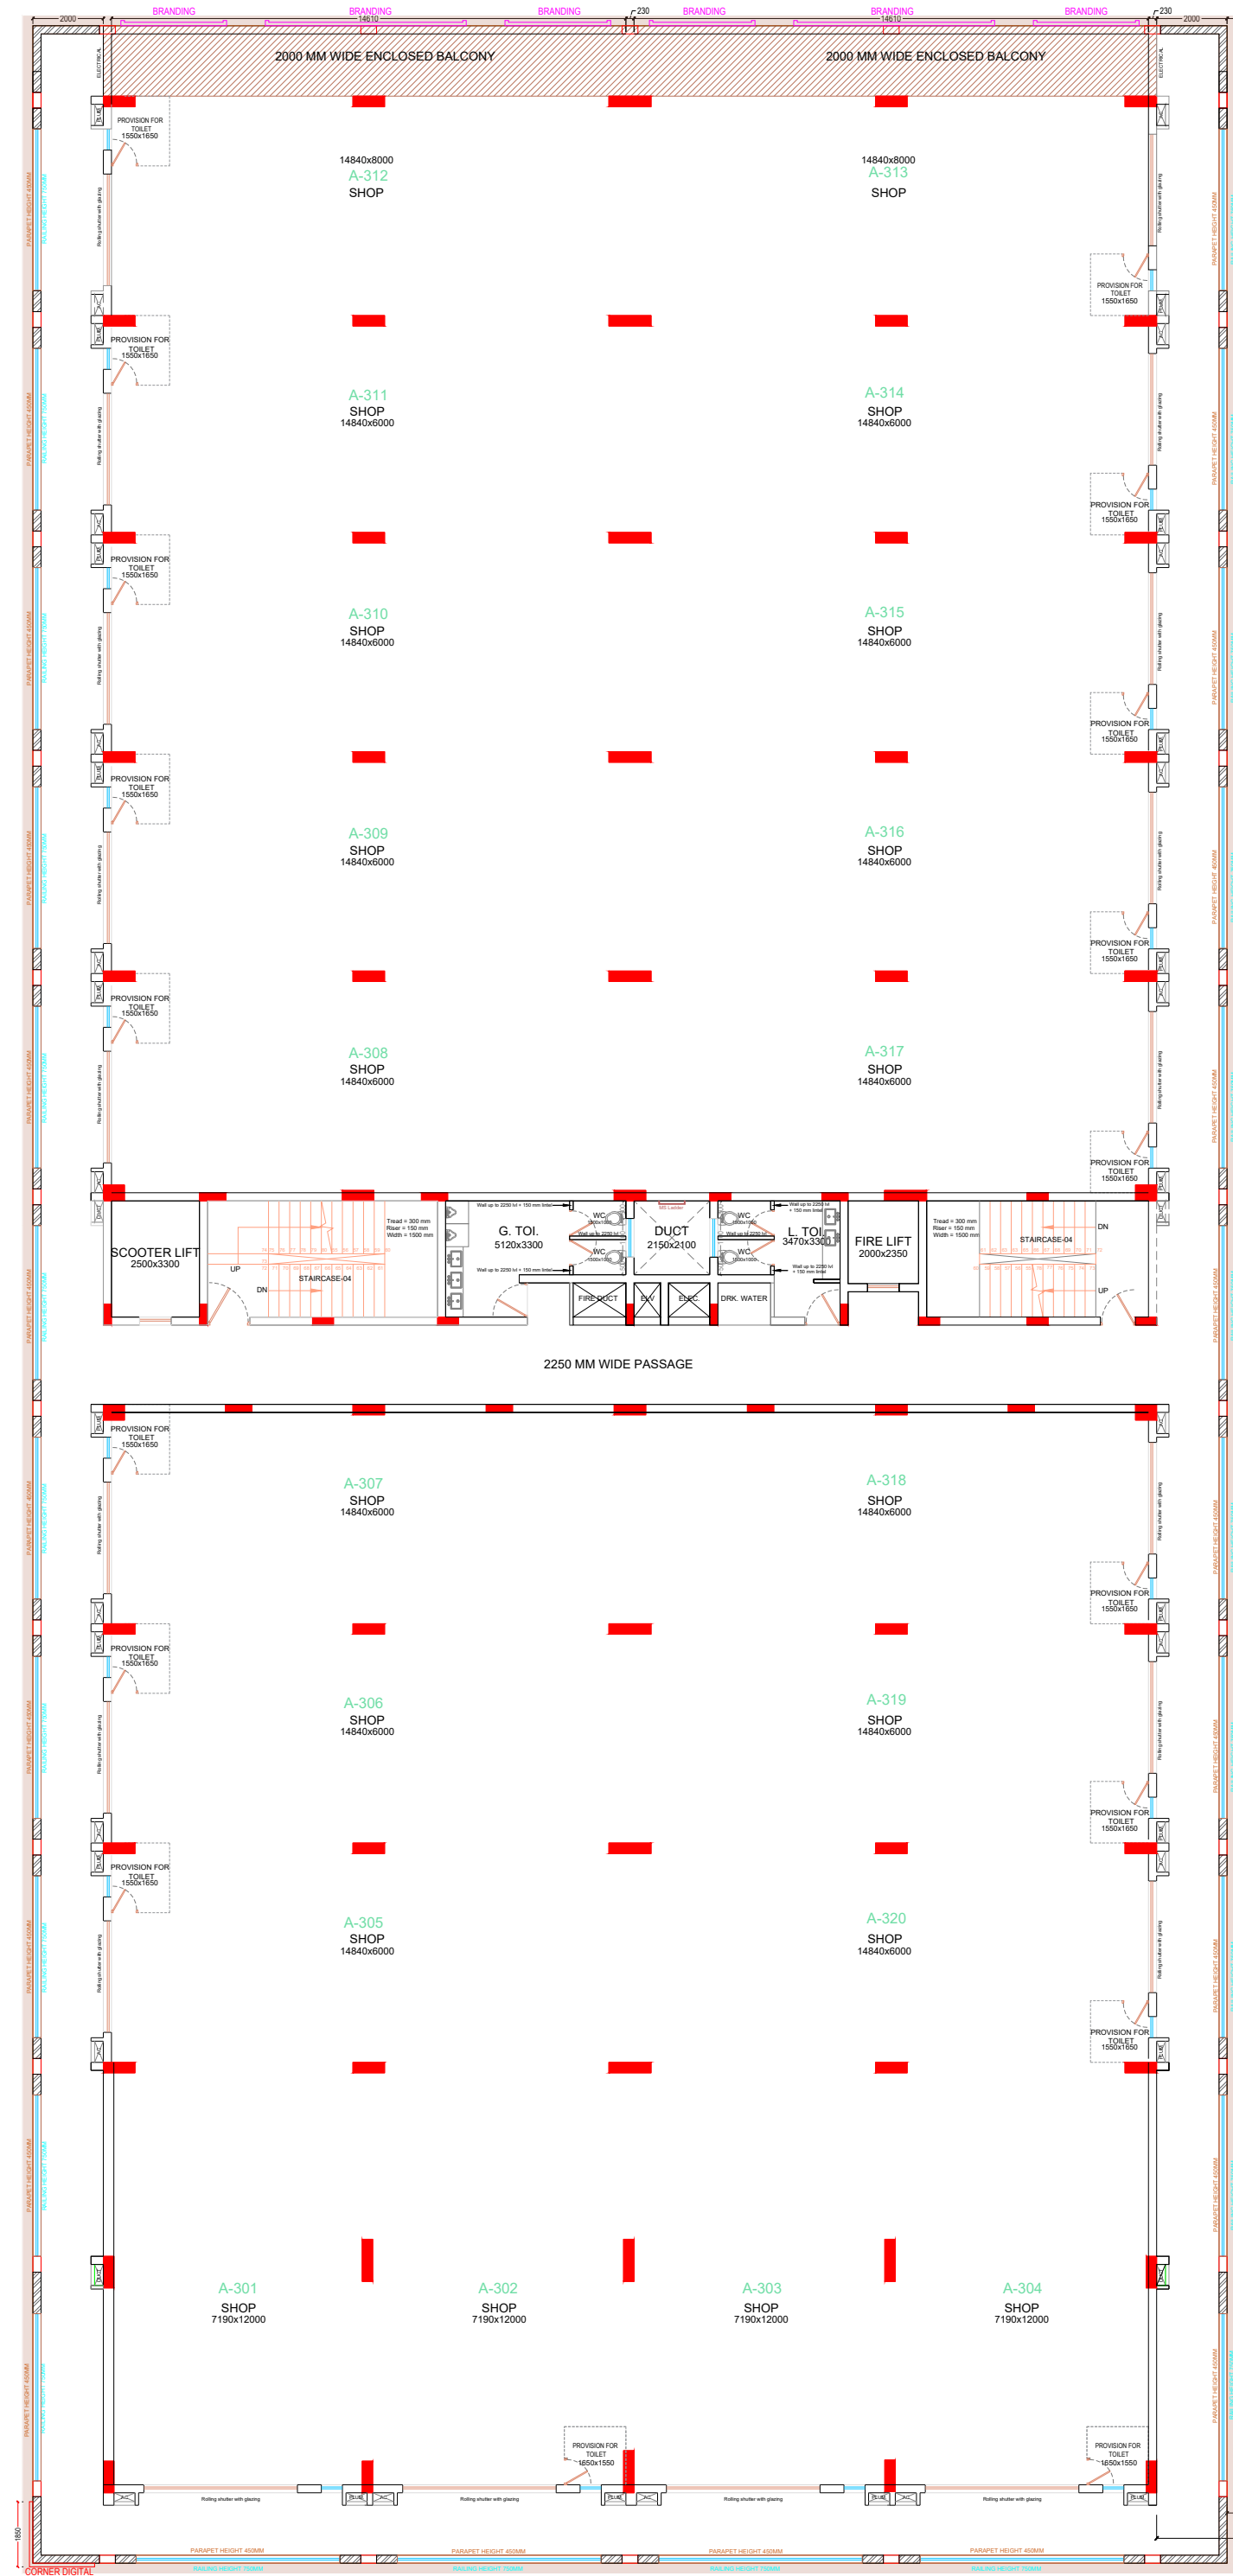

THIRD FLOOR
WING A

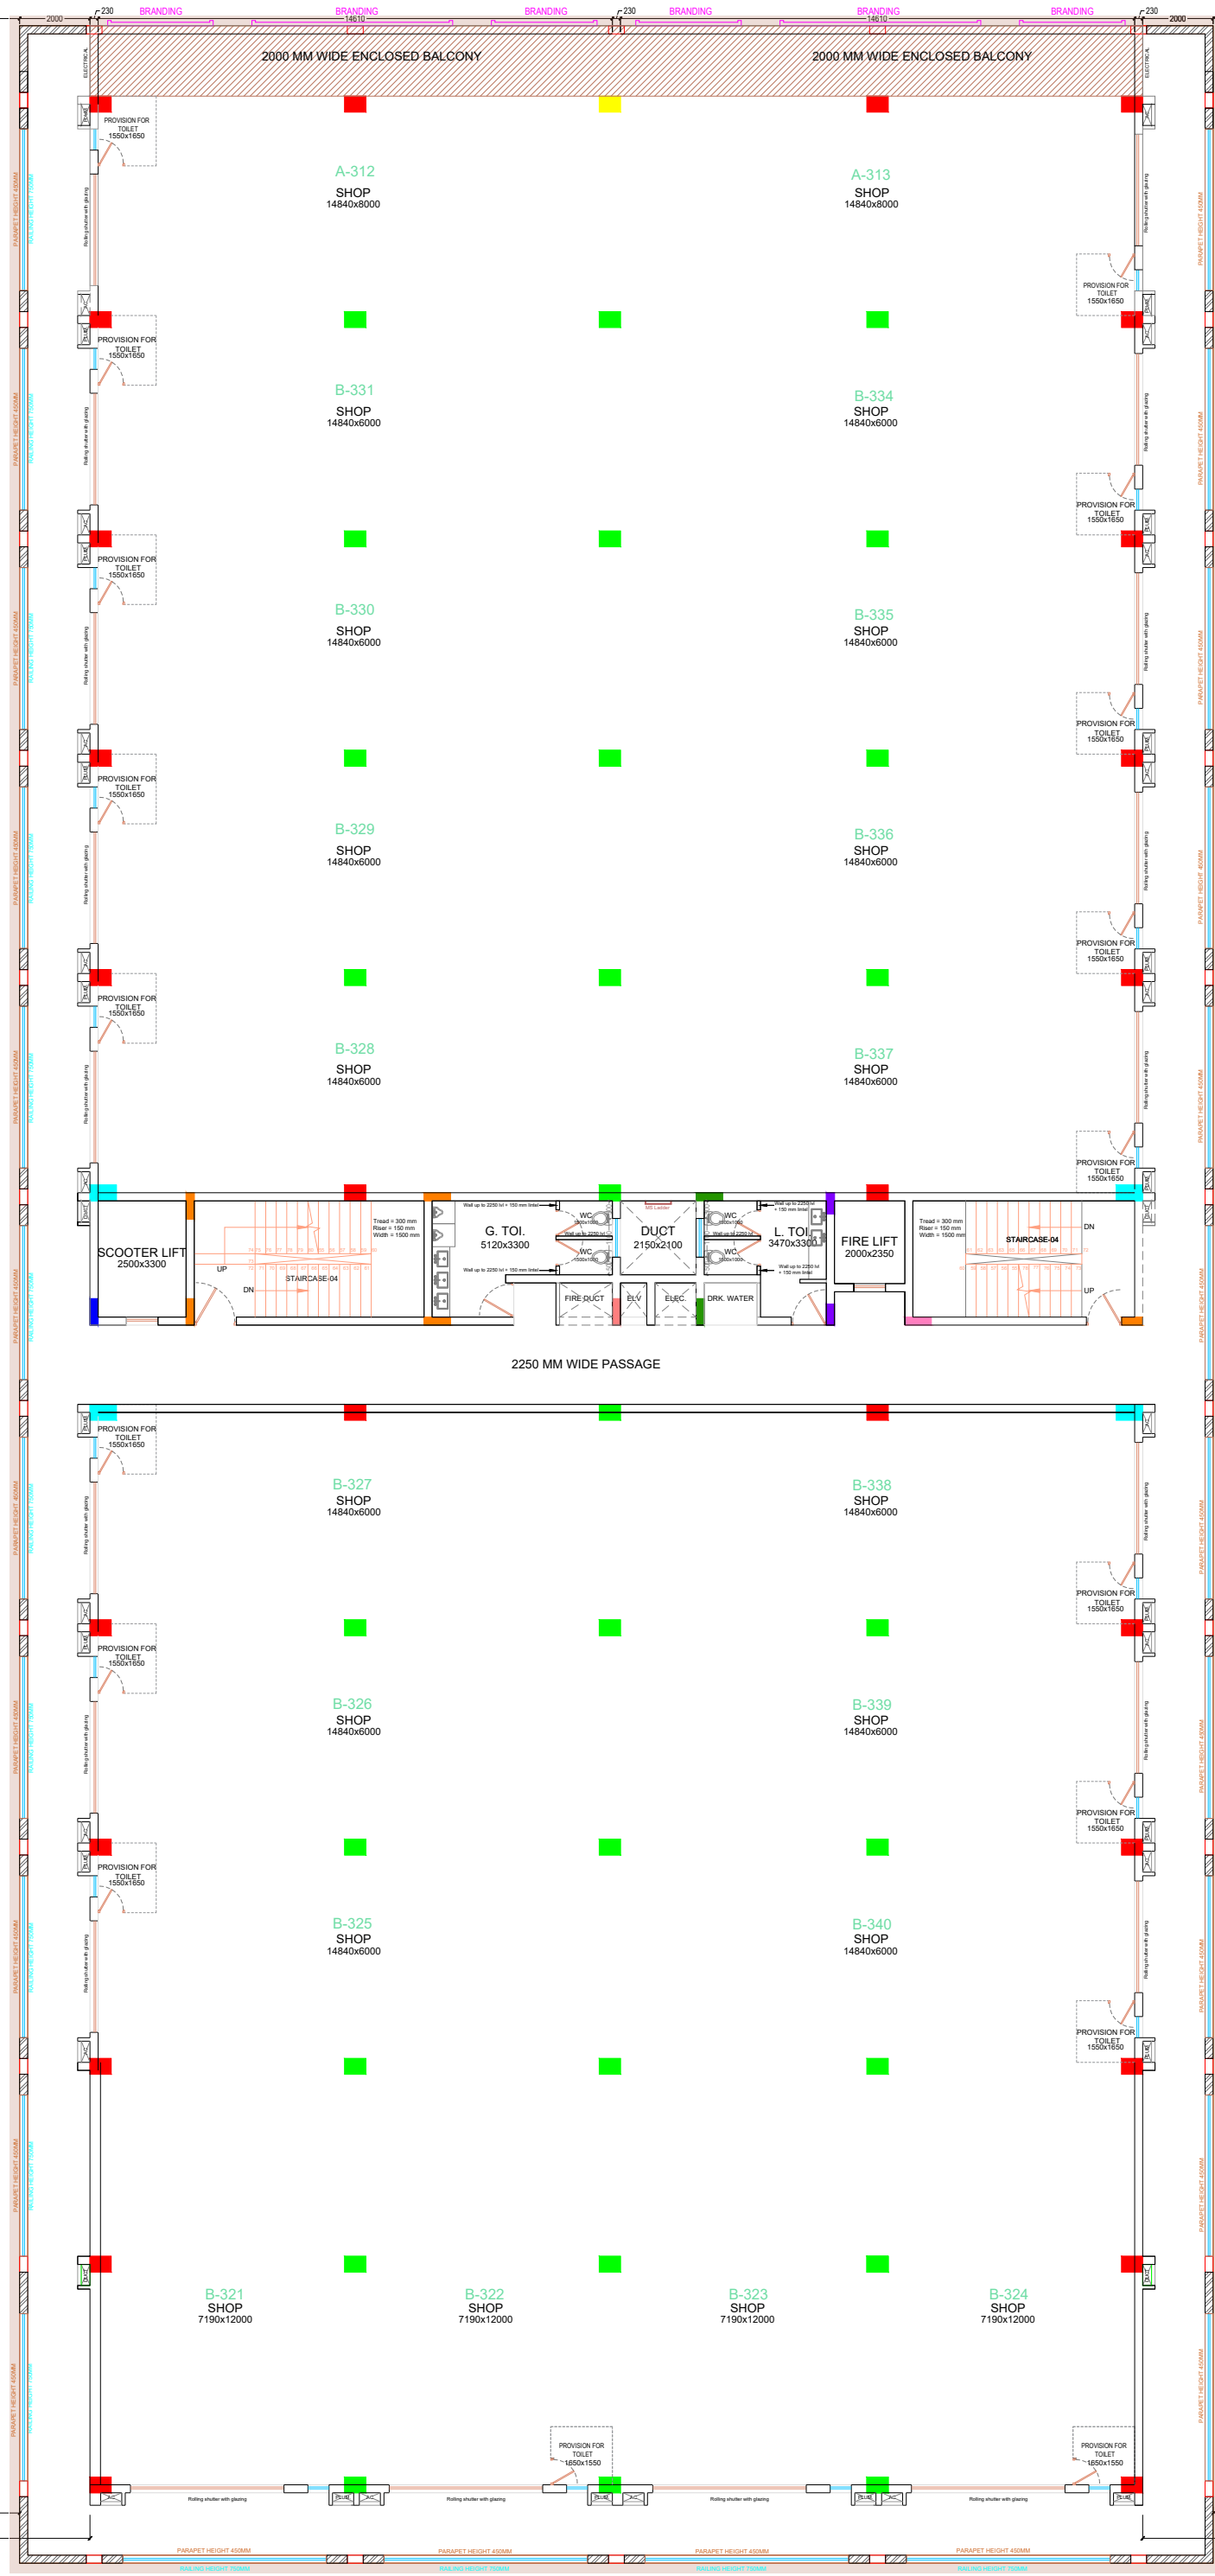

THIRD FLOOR
WING B

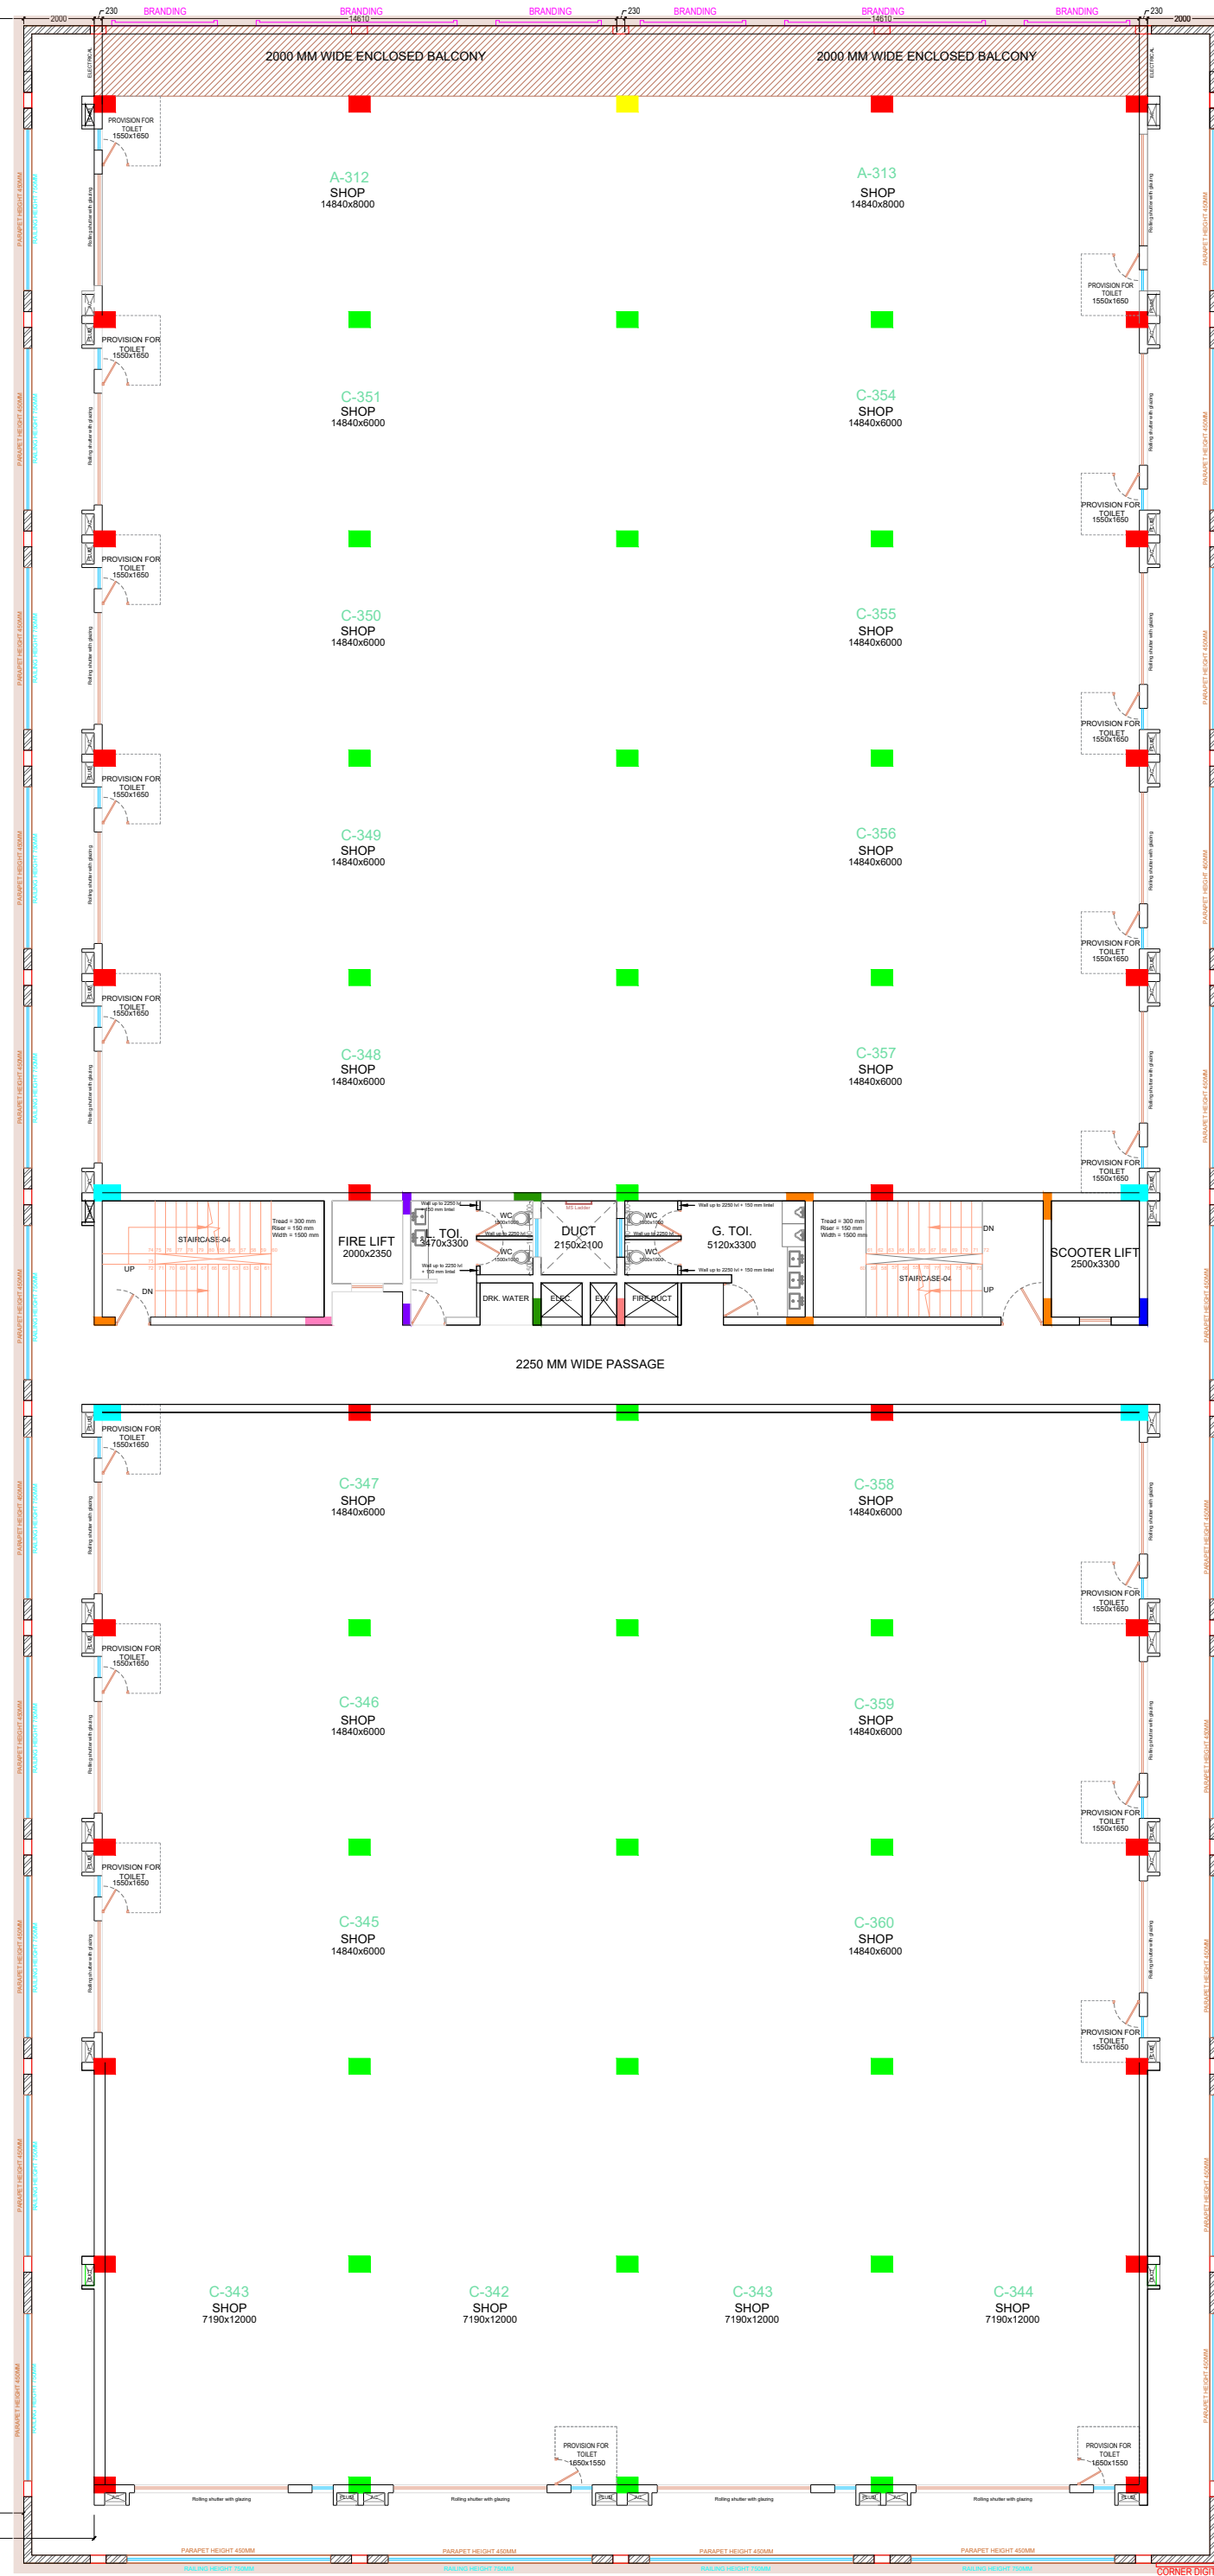

THIRD FLOOR
WING C

STAGE:
WORKING DRAWING

SHEET:
A1

PURPOSE:
ADVANCE COPY

COPYRIGHT:
THIS DRAWING IS A COPYRIGHT AND MUST NOT BE DISCLOSED, USED OR REPRODUCED IN ANY FORM WITHOUT THE EXPRESS PERMISSION FROM DISHA VISION.

- GENERAL NOTES:
- DO NOT SCALE THIS DRAWING.
 - ALL THE WRITTEN DIMENSIONS TO BE FOLLOWED.
 - ALL DIMENSIONS ARE IN MM UNLESS OTHERWISE SPECIFIED.
 - ALL THE DIMENSIONS ARE UNFINISHED UNLESS OTHERWISE SPECIFIED.
 - THE SIZES MENTIONED IN SCHEDULE FOR DOORS, WINDOWS & OPENINGS ARE CLEAR MASONRY OPENING SIZES.
 - ANY DISCREPANCY FOUND IN THIS DRAWING SHOULD BE BROUGHT TO THE NOTICE OF THE ARCHITECT BEFORE THE EXECUTION OF WORK.
 - THIS DRAWINGS SHALL BE REFERRED WITH DETAILS, STRUCTURAL, SERVICES AND OTHER RELEVANT DRAWINGS.
 - "DISHA VISION" SHALL NOT BE RESPONSIBLE IN ANY MANNER FOR THE CENTERING, SHUTTERING AND SCAFFOLDING ERECTED AT SITE FOR STRUCTURAL PURPOSE.
 - ALL THE LEVELS SPECIFIED ARE SFL (STRUCTURAL FINISH LEVEL) UNLESS OTHERWISE SPECIFIED.
 - ANY ADDITIONAL EXCAVATION / PROVISION REQUIRED FOR THE PURPOSE OF SOLING, WATERPROOFING, COMPACTION, RAFT SHALL BE AS PER THE DRAWING AND DETAILS GIVEN BY THE STRUCTURAL CONSULTANT & WATERPROOFING AGENCIES.

SCHEDULE FOR OPENINGS:

CONSULTANTS:

STRUCTURAL: PCPL, NAGPUR
ELECTRICAL: JHAVERI ASSOCIATES, AHMEDABAD
PLUMBING: JHAVERI ASSOCIATES, AHMEDABAD
FIRE FIGHTING: JHAVERI ASSOCIATES, AHMEDABAD
HVAC: ---
LANDSCAPE: ---

MASONRY DETAILS:

230/200 MM THICK WALL
150 MM THICK WALL
100 MM THICK WALL
LOW HEIGHT WALL

R8	---
R7	---
R6	---
R5	---
R4	---
R3	---
R2	---
R1	05-10-24 Brick work layout & door window schedule
R0	09-11-23 1st draft for structural co-ordination at site

REVISIONS:

PROJECT:
KARAN KOTHARI BUSINESS PARK

TITLE:
PLOT 1 - THIRD FLOOR PLAN

SCALE:	1:175	NORTH:
DATE:		
DRAWN BY:		
CHECKED BY:	Akash M.	
DRAWING NO.:	---	

AKASH MOHOTA
+91 7276094577
akash.dishavision@outlook.com
www.dishavision.com
@dishavision
1st Floor, Monalisa Complex,
Opp. to Rajawade Police Station,
Amravati - 444601

STAGE:
WORKING DRAWING

SHEET:
A1

PURPOSE:
ADVANCE COPY

COPYRIGHT:
THIS DRAWING IS A COPYRIGHT AND MUST NOT BE DISCLOSED, USED OR REPRODUCED IN ANY FORM WITHOUT THE EXPRESS PERMISSION FROM DISHA VISION.

- GENERAL NOTES:
- DO NOT SCALE THIS DRAWING.
 - ALL THE WRITTEN DIMENSIONS TO BE FOLLOWED.
 - ALL DIMENSIONS ARE IN MM UNLESS OTHERWISE SPECIFIED.
 - ALL THE DIMENSIONS ARE UNFINISHED UNLESS OTHERWISE SPECIFIED.
 - THE SIZES MENTIONED IN SCHEDULE FOR DOORS, WINDOWS & OPENINGS ARE CLEAR MASONRY OPENING SIZES.
 - ANY DISCREPANCY FOUND IN THIS DRAWING SHOULD BE BROUGHT TO THE NOTICE OF THE ARCHITECT BEFORE THE EXECUTION OF WORK.
 - THIS DRAWINGS SHALL BE REFERRED WITH DETAILS, STRUCTURAL SERVICES AND OTHER RELEVANT DRAWINGS.
 - "DISHA VISION" SHALL NOT BE RESPONSIBLE IN ANY MANNER FOR THE CENTERING, SHUTTERING AND SCAFFOLDING ERECTED AT SITE FOR STRUCTURAL PURPOSE.
 - ALL THE LEVELS SPECIFIED ARE SFL (STRUCTURAL FINISH LEVEL) UNLESS OTHERWISE SPECIFIED.
 - ANY ADDITIONAL EXCAVATION / PROVISION REQUIRED FOR THE PURPOSE OF SOLING, WATERPROOFING, COMPACTION, RAFT SHALL BE AS PER THE DRAWING AND DETAILS GIVEN BY THE STRUCTURAL CONSULTANT & WATERPROOFING AGENCIES.

SCHEDULE FOR OPENINGS:

CONSULTANTS:
STRUCTURAL: POPLI NAGPUR
ELECTRICAL: JHAVERI ASSOCIATES, AHMEDABAD
PLUMBING: JHAVERI ASSOCIATES, AHMEDABAD
FIRE FIGHTING: JHAVERI ASSOCIATES, AHMEDABAD
HVAC: ---
LANDSCAPE: ---

MASONRY DETAILS:
230/200 MM THICK WALL
150 MM THICK WALL
100 MM THICK WALL
LOW HEIGHT WALL

R8	---
R7	---
R6	---
R5	---
R4	---
R3	---
R2	---
R1	05-10-24 Brick work layout & door window schedule
R0	09-11-23 1st draft for structural co-ordination at site
REVISIONS:	


PROJECT:
KARAN KOTHARI BUSINESS PARK

TITLE:
PLOT 2 - GROUND FLOOR PLAN


SCALE:	1:175	NORTH: N
DATE:		
DRAWN BY:		
CHECKED BY:	Akash M.	
DRAWING NO.:	---	

AKASH MOHOTA
+91 7276094577
akash.dishavision@outlook.com
www.dishavision.com
@dishavision
1st Floor, Monalisa Complex,
Opp. to Rajawade Police Station,
Amravati - 444601


DISHA
VISION
INNOVATE. DESIGN. BUILD

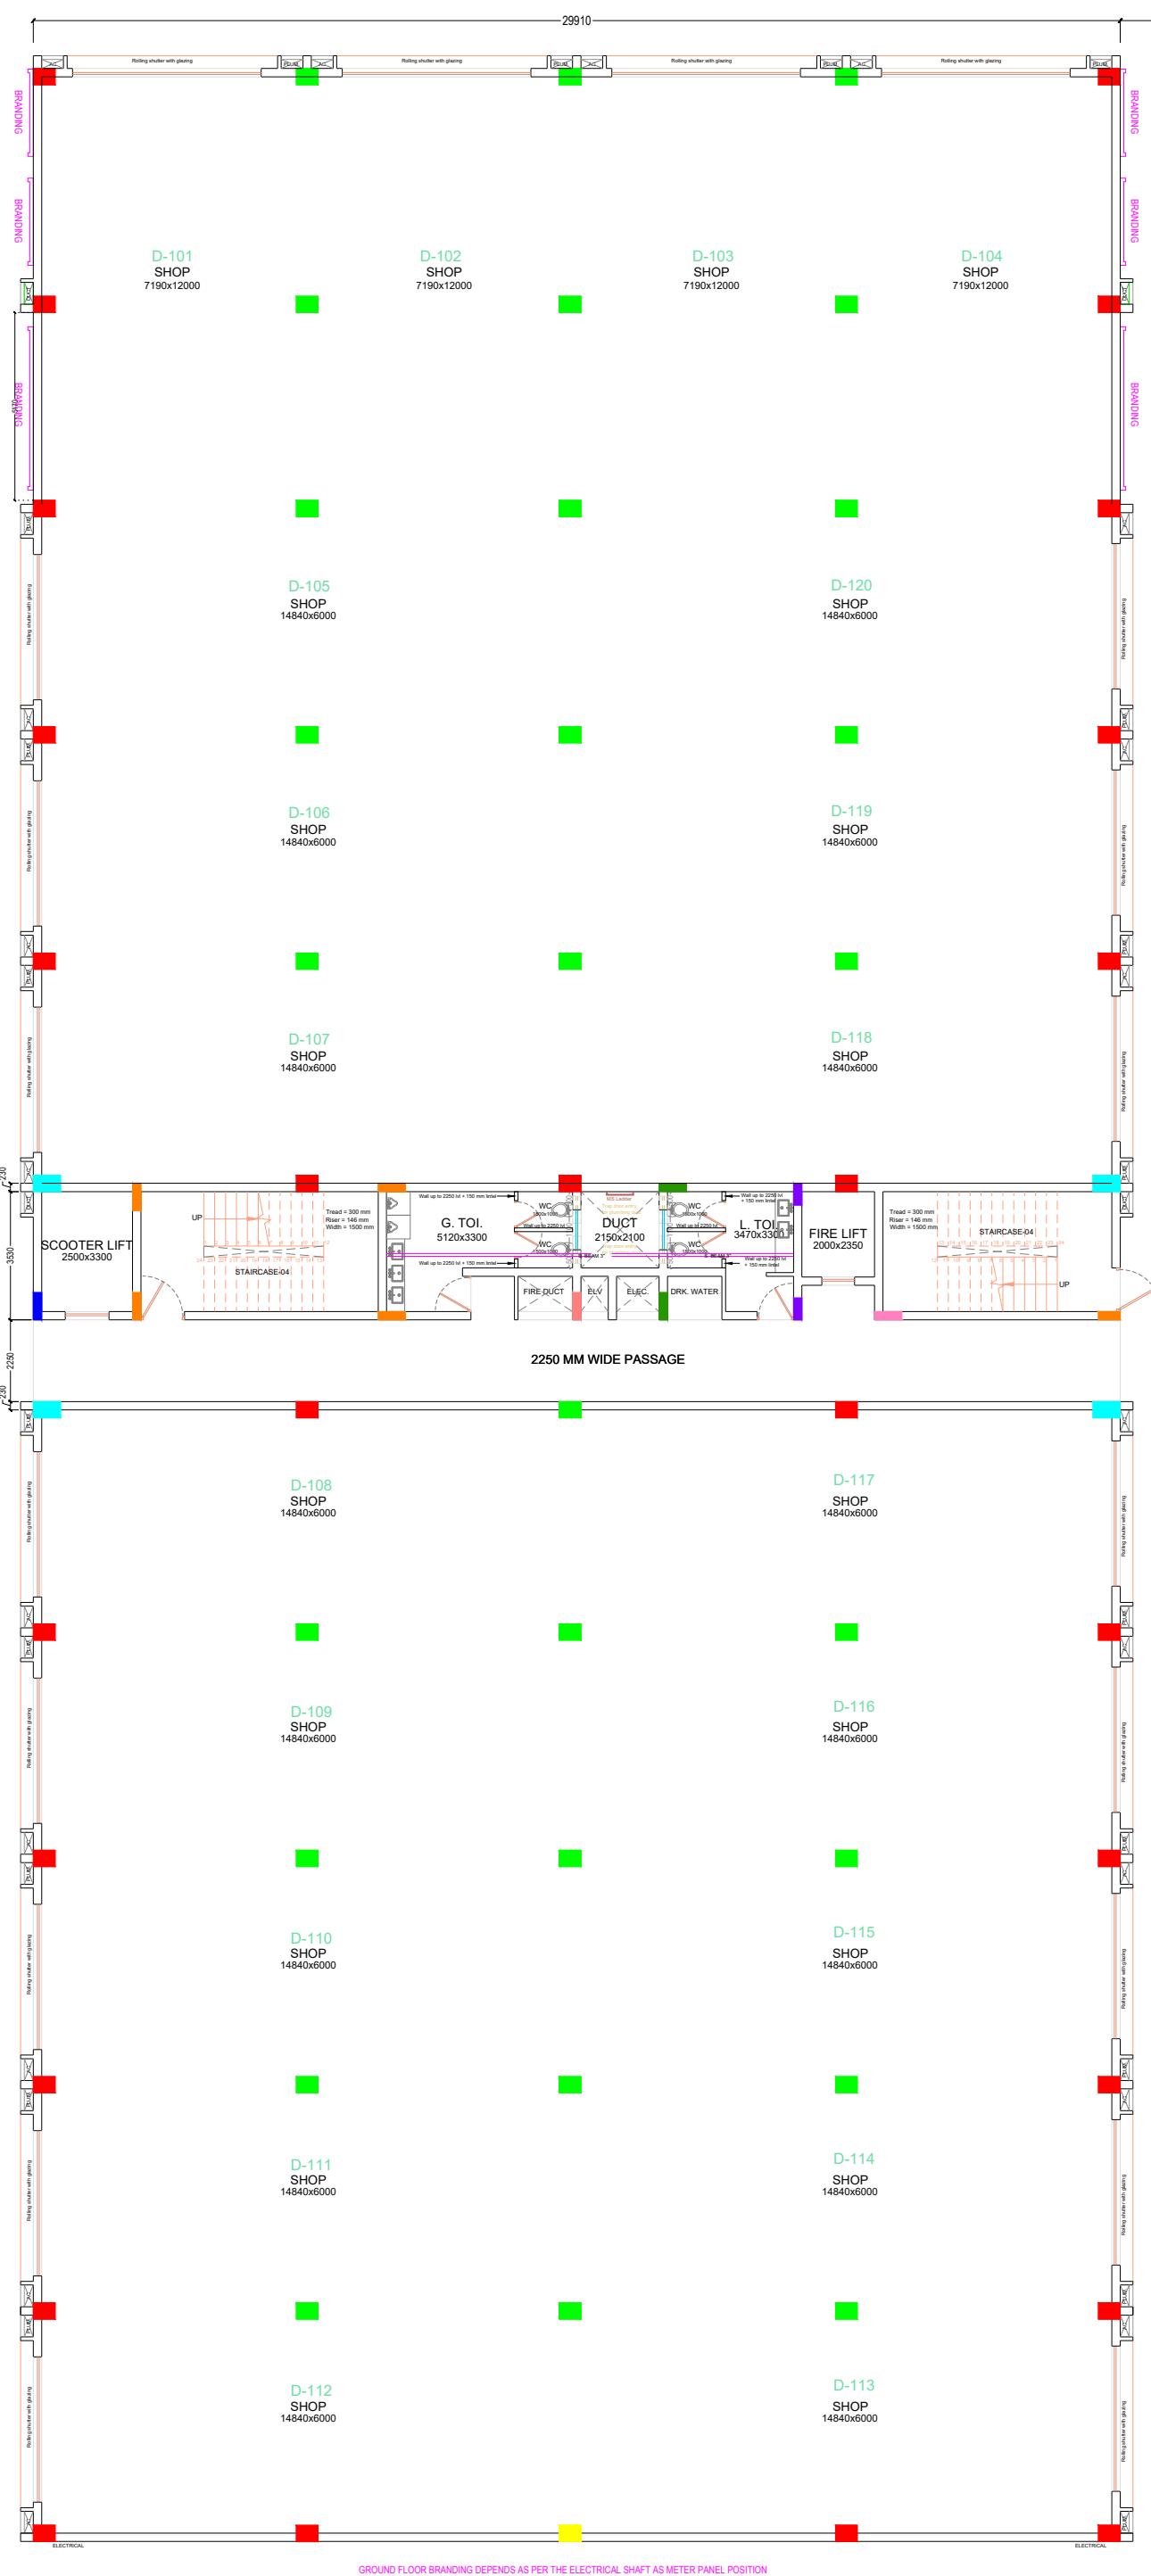


GROUND FLOOR
WING D

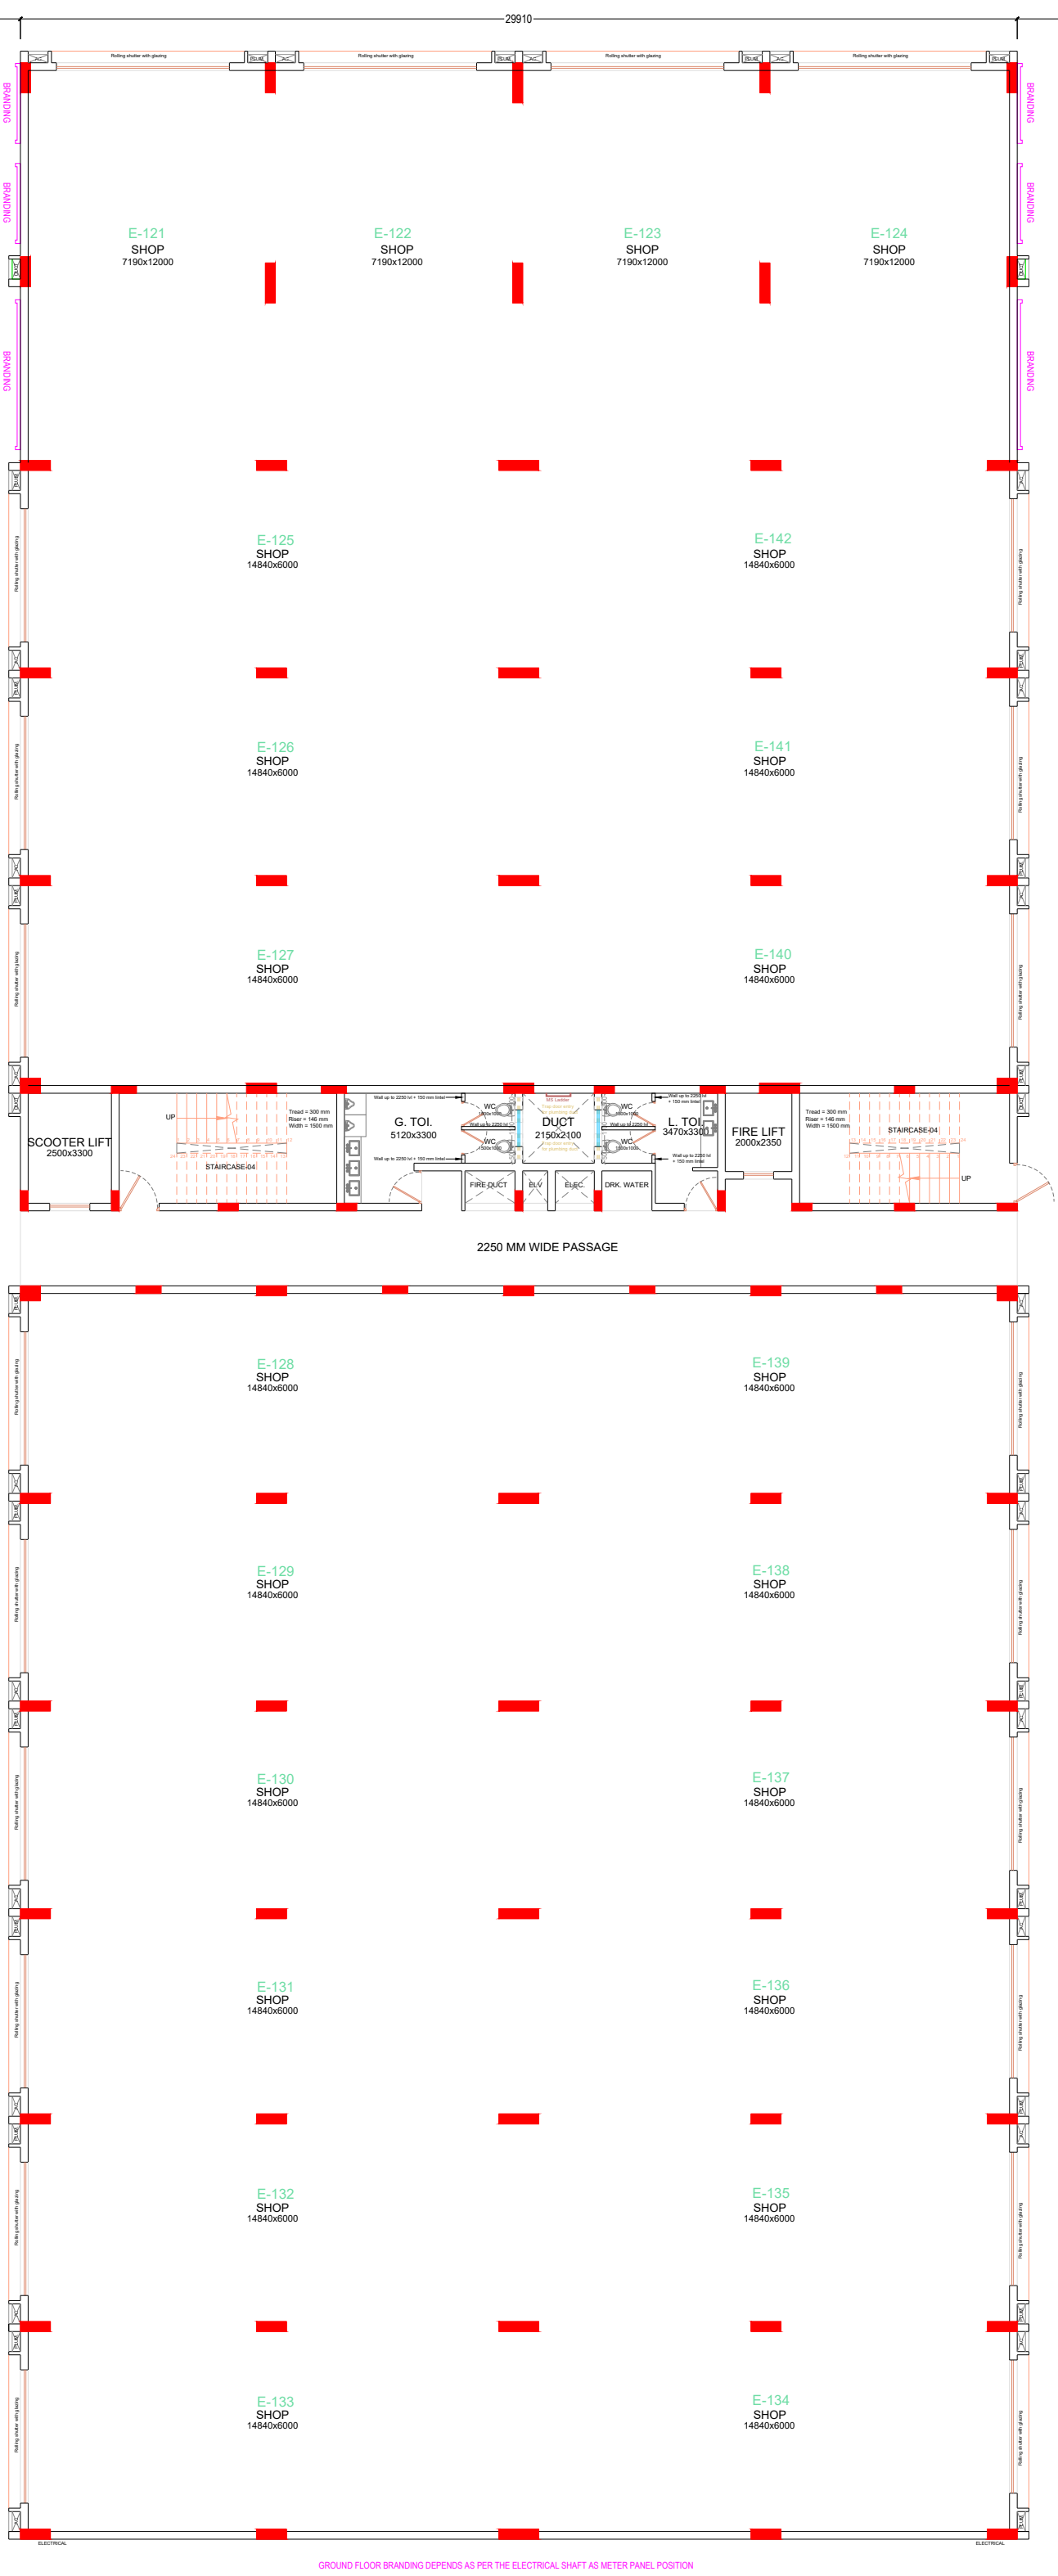


GROUND FLOOR
WING E

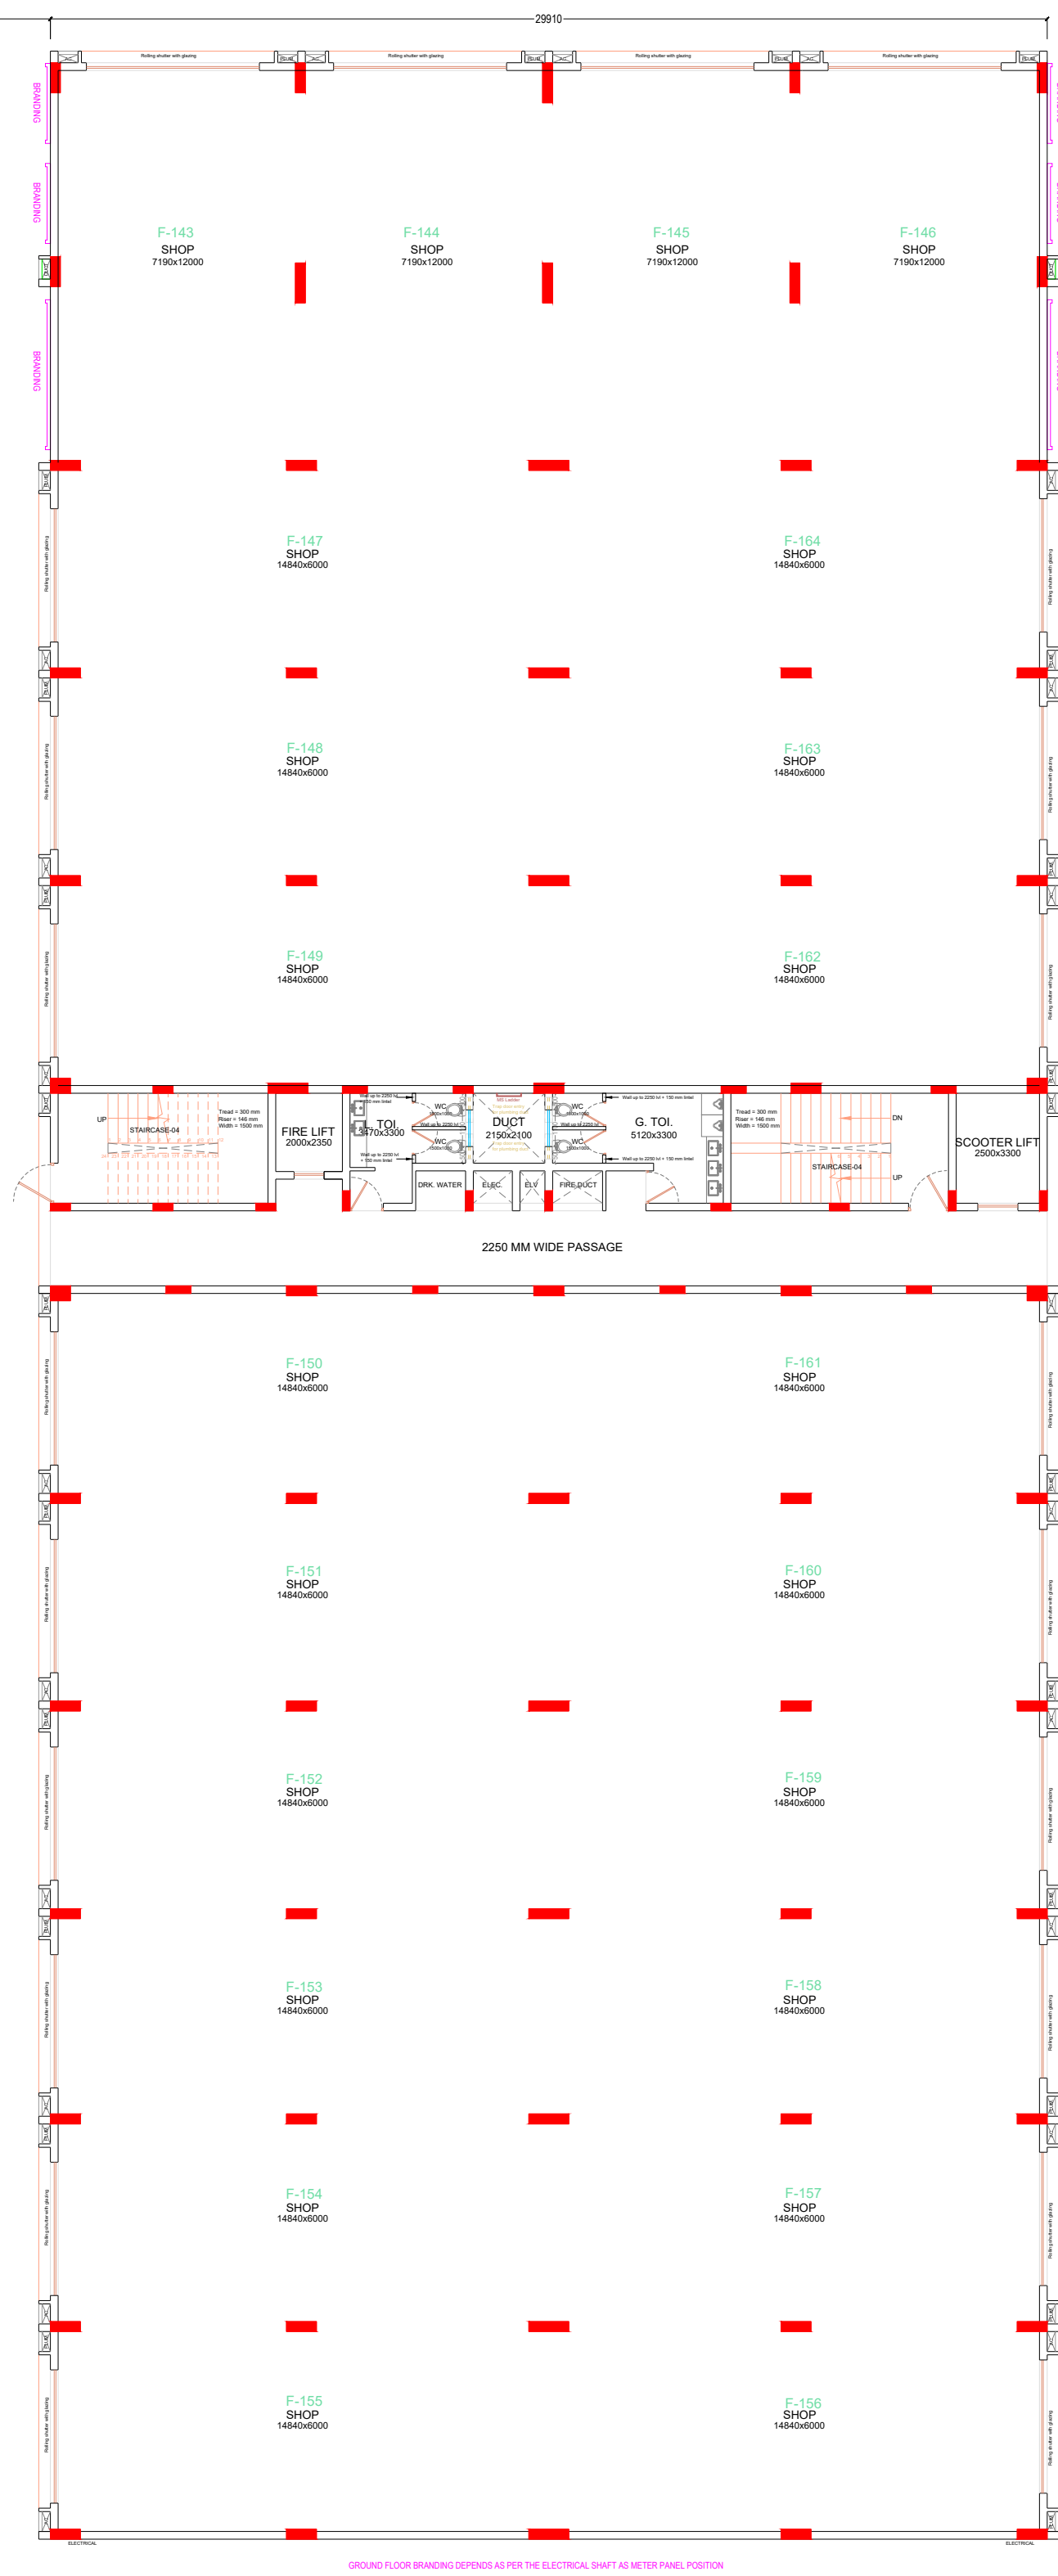


GROUND FLOOR
WING F

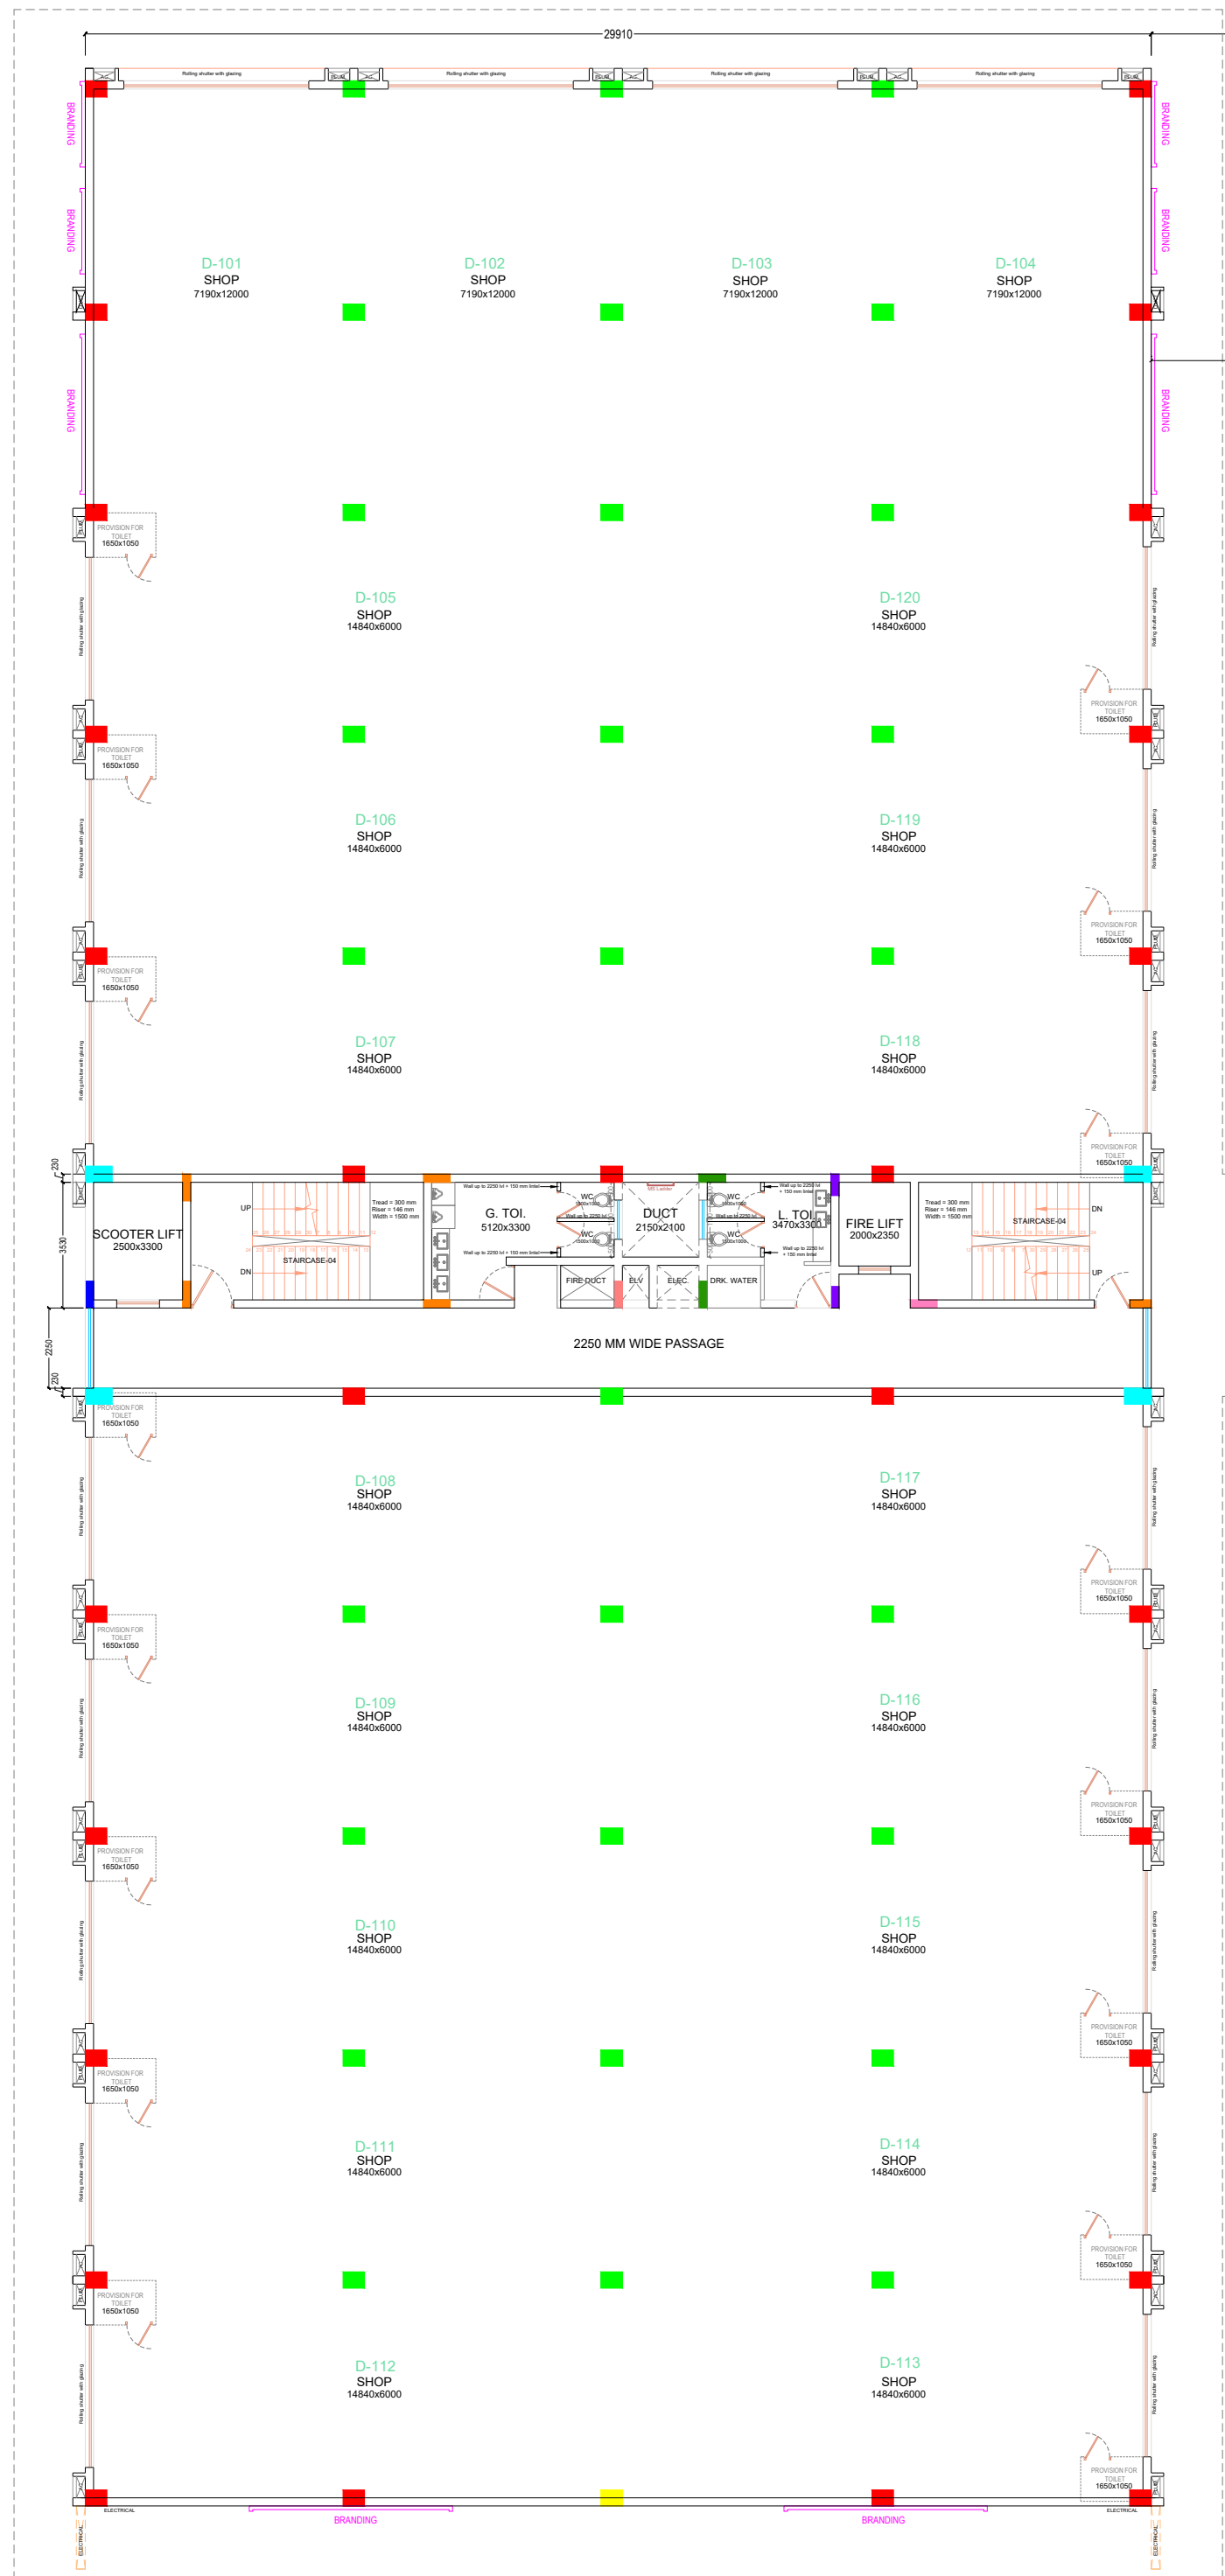

FIRST FLOOR
WING D

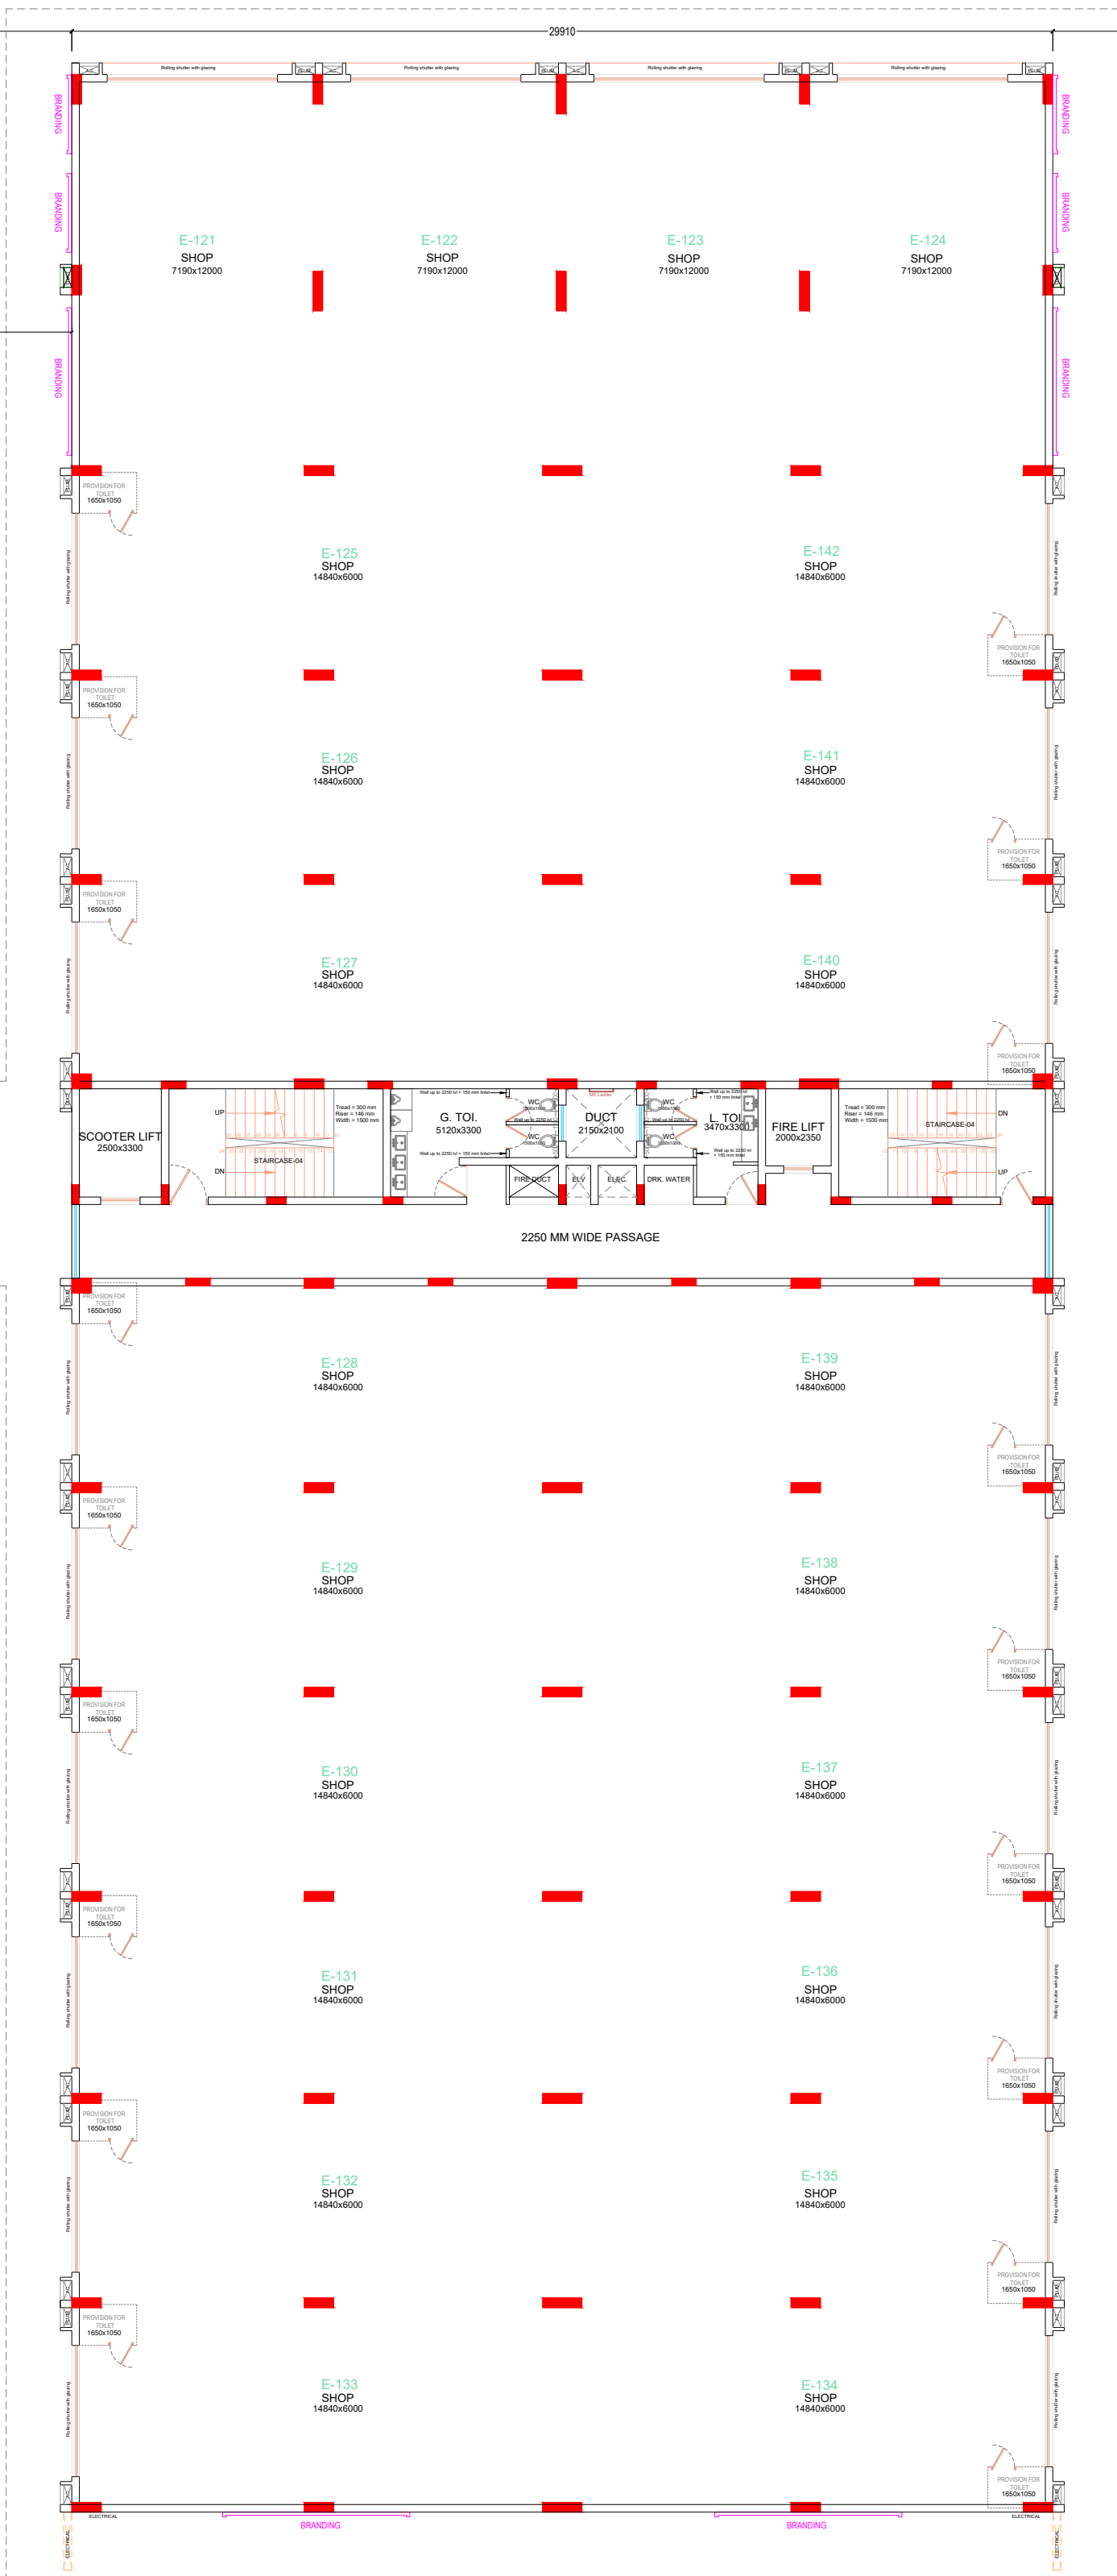

FIRST FLOOR
WING E

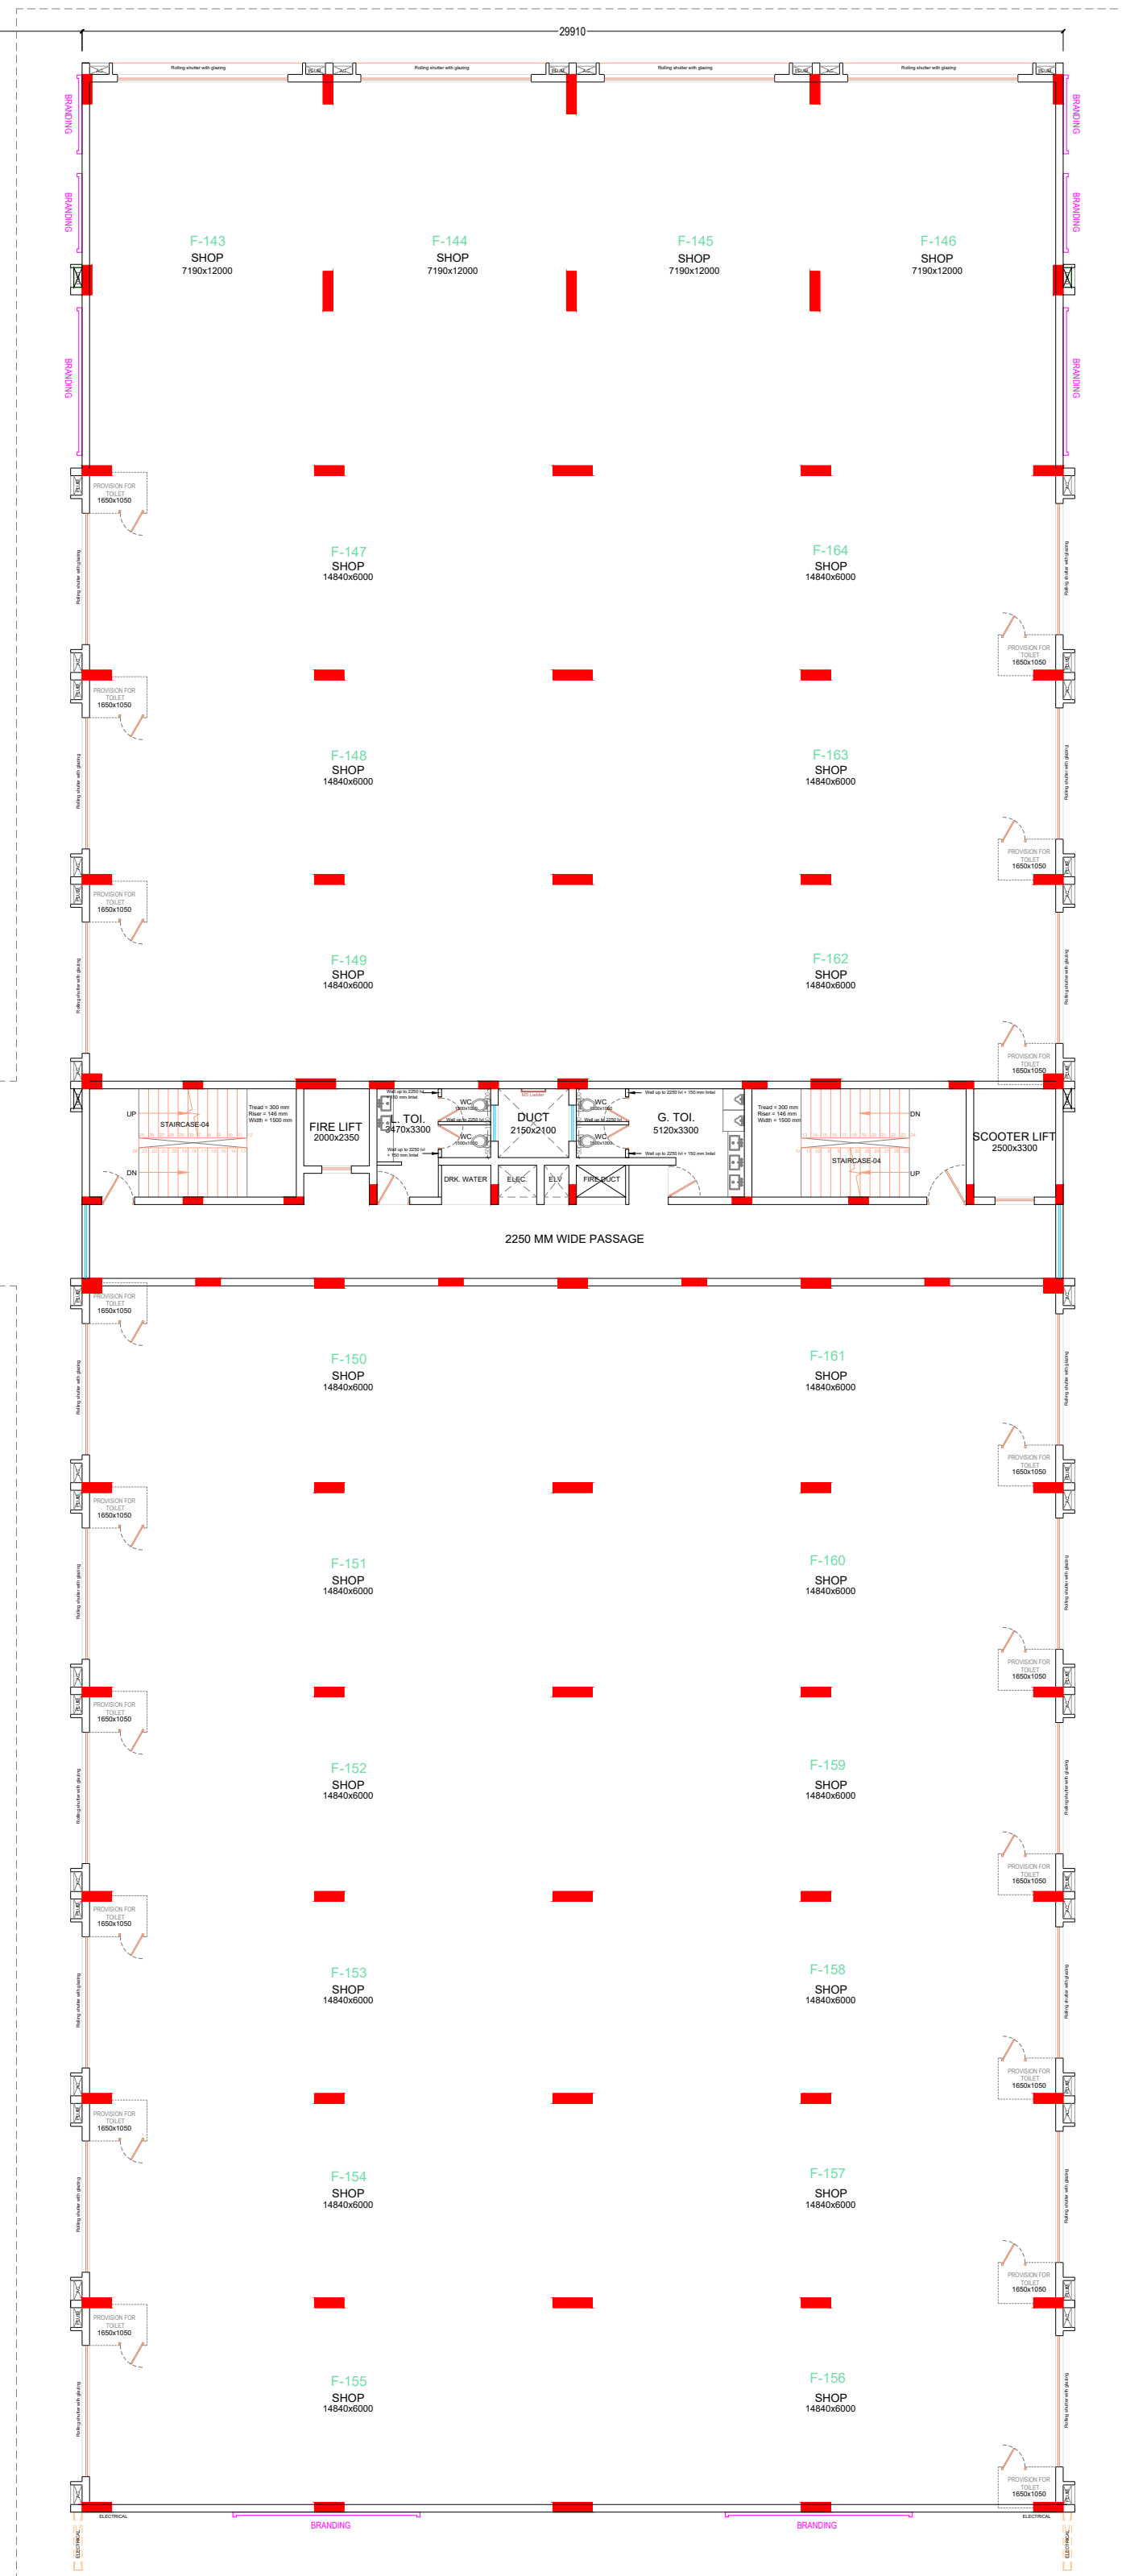

FIRST FLOOR
WING F

STAGE:
WORKING DRAWING

SHEET:
A1

PURPOSE:
ADVANCE COPY

COPYRIGHT:
THIS DRAWING IS A COPYRIGHT AND MUST NOT BE DISCLOSED, USED OR REPRODUCED IN ANY FORM WITHOUT THE EXPRESS PERMISSION FROM DISHA VISION.

- GENERAL NOTES:
- DO NOT SCALE THIS DRAWING.
 - ALL THE WRITTEN DIMENSIONS TO BE FOLLOWED.
 - ALL DIMENSIONS ARE IN MM UNLESS OTHERWISE SPECIFIED.
 - ALL THE DIMENSIONS ARE UNFINISHED UNLESS OTHERWISE SPECIFIED.
 - THE SIZES MENTIONED IN SCHEDULE FOR DOORS, WINDOWS & OPENINGS ARE CLEAR MASONRY OPENING SIZES.
 - ANY DISCREPANCY FOUND IN THIS DRAWING SHOULD BE BROUGHT TO THE NOTICE OF THE ARCHITECT BEFORE THE EXECUTION OF WORK.
 - THIS DRAWINGS SHALL BE REFERRED WITH DETAILS, STRUCTURAL SERVICES AND OTHER RELEVANT DRAWINGS.
 - "DISHA VISION" SHALL NOT BE RESPONSIBLE IN ANY MANNER FOR THE CENTERING, SHUTTERING AND SCAFFOLDING ERECTED AT SITE FOR STRUCTURAL PURPOSE.
 - ALL THE LEVELS SPECIFIED ARE SFL (STRUCTURAL FINISH LEVEL) UNLESS OTHERWISE SPECIFIED.
 - ANY ADDITIONAL EXCAVATION / PROVISION REQUIRED FOR THE PURPOSE OF SOLING, WATERPROOFING, COMPACTION, RAFT SHALL BE AS PER THE DRAWING AND DETAILS GIVEN BY THE STRUCTURAL CONSULTANT & WATERPROOFING AGENCIES.

SCHEDULE FOR OPENINGS:

CONSULTANTS:
STRUCTURAL: POPL, NAGPUR
ELECTRICAL: JHAVERI ASSOCIATES, AHMEDABAD
PLUMBING: JHAVERI ASSOCIATES, AHMEDABAD
FIRE FIGHTING: JHAVERI ASSOCIATES, AHMEDABAD
HVAC: ---
LANDSCAPE: ---

MASONRY DETAILS:
230/200 MM THICK WALL
150 MM THICK WALL
100 MM THICK WALL
LOW HEIGHT WALL


R8	---
R7	---
R6	---
R5	---
R4	---
R3	---
R2	---
R1	05-10-24 Brick work layout & door window schedule
R0	09-11-23 1st draft for structural co-ordination at site
REVISIONS:	

PROJECT:
KARAN KOTHARI BUSINESS PARK


TITLE:
PLOT 2 - FIRST FLOOR PLAN

SCALE:	1:175	NORTH:
DATE:		
DRAWN BY:		
CHECKED BY:	Akash M.	
DRAWING NO.:	---	


AKASH MOHOTA
+91 7276094577
akash.dishavision@outlook.com
www.dishavision.com
@dishavision
1st Floor, Monalisa Complex,
Opp. to Rajawade Police Station,
Amravati - 444601

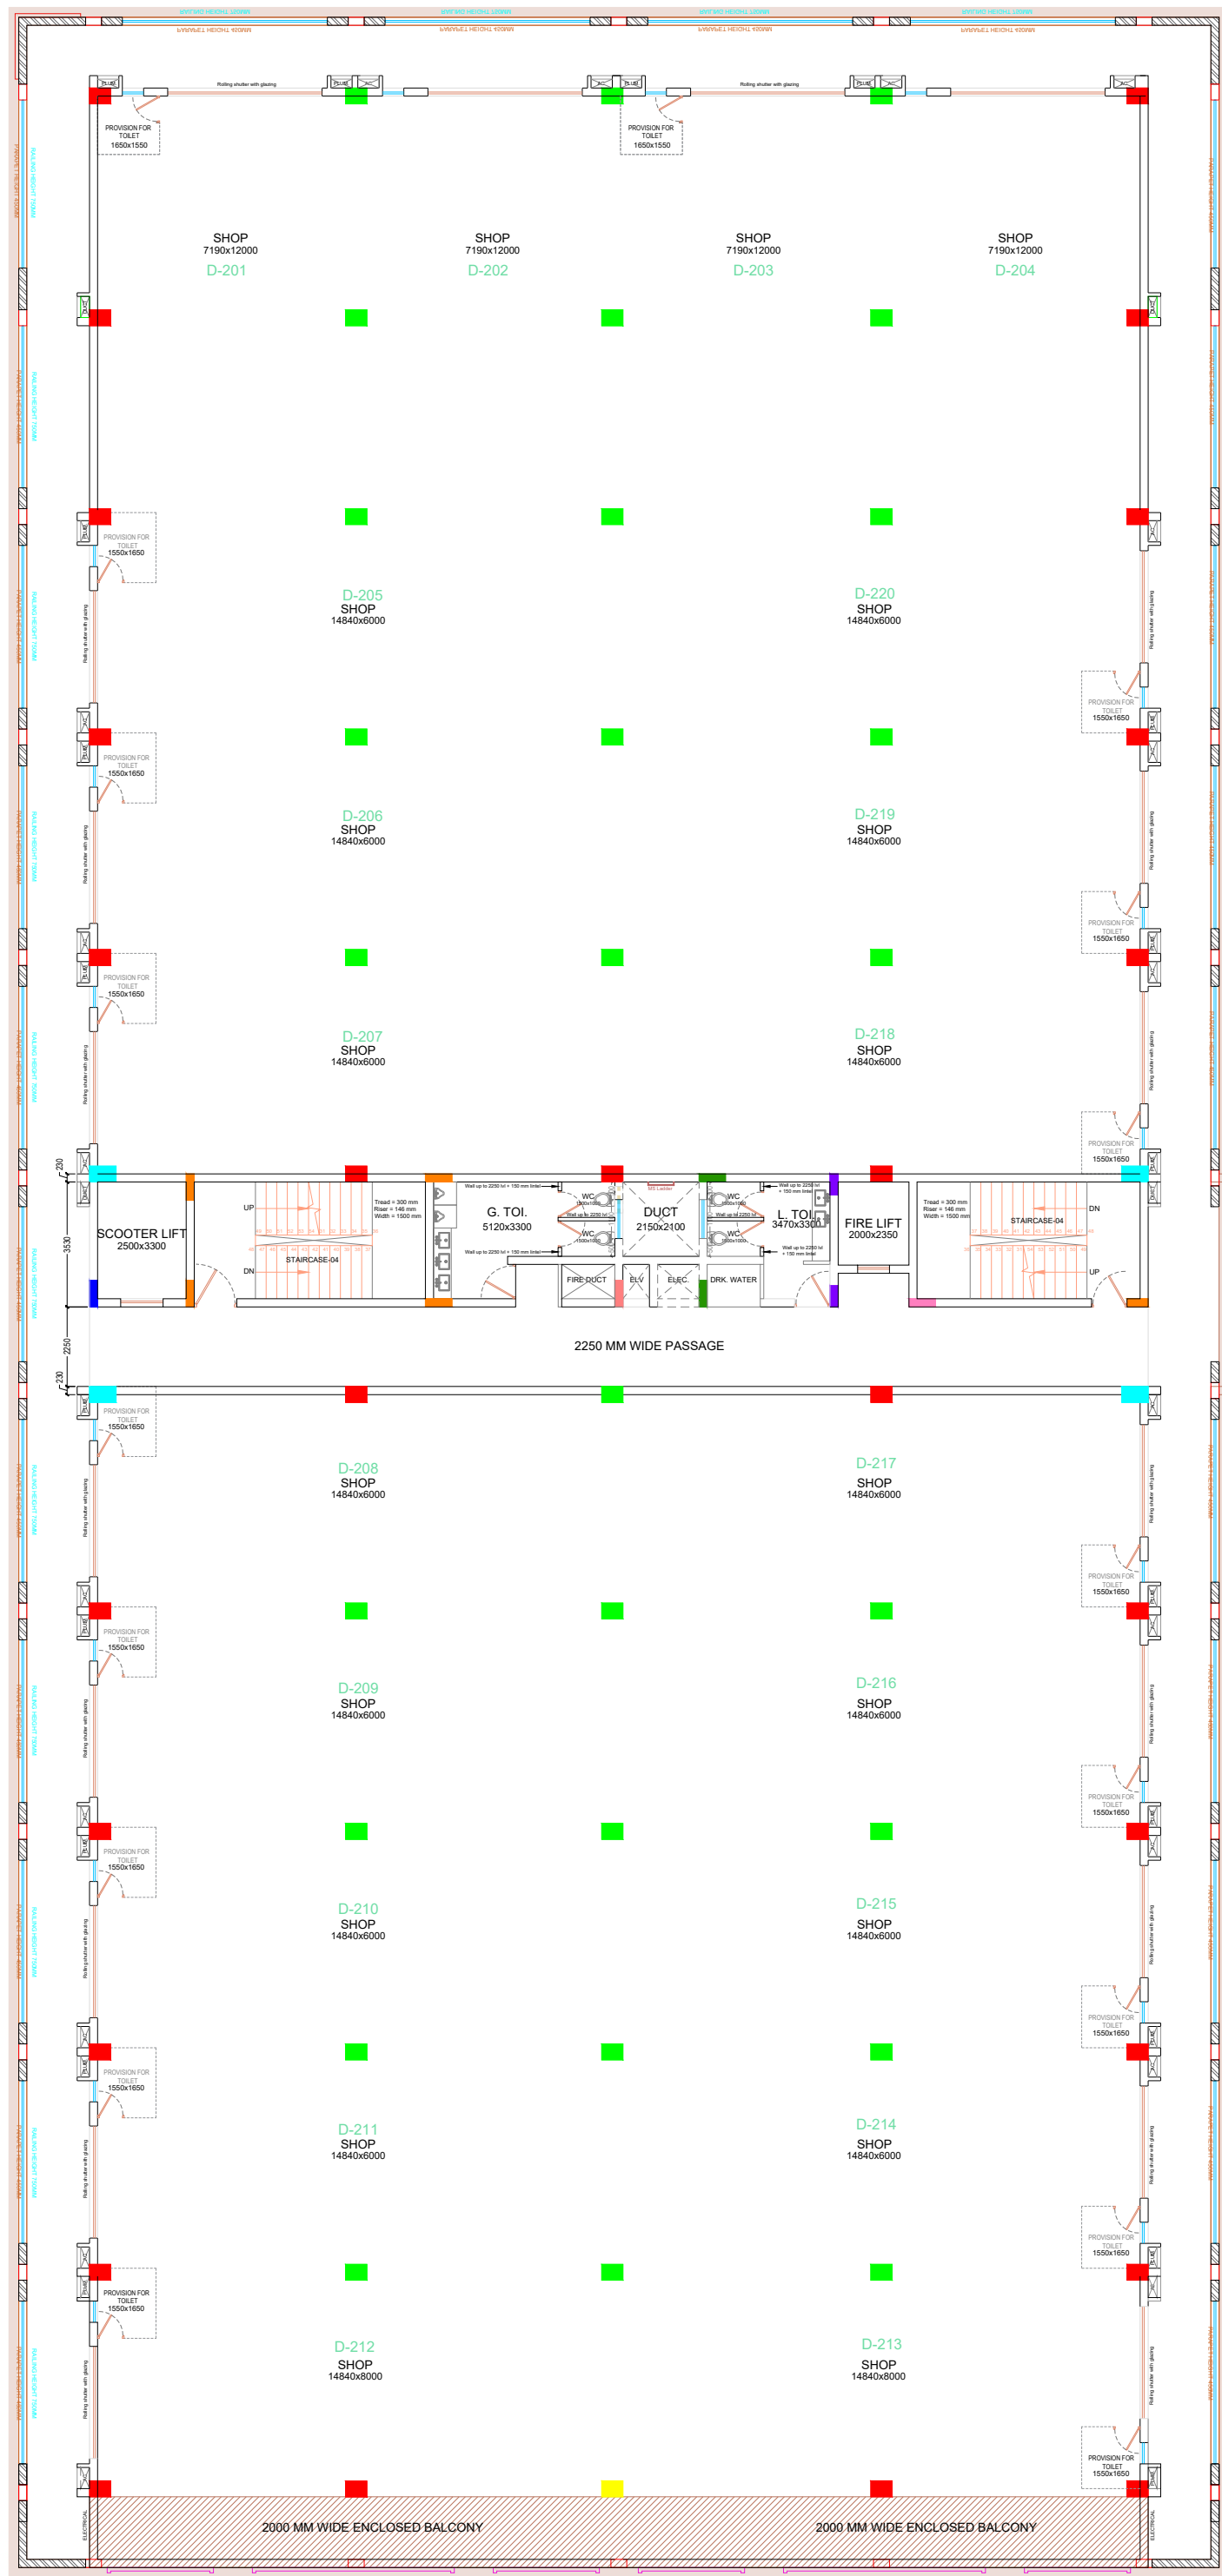

SECOND FLOOR
WING D

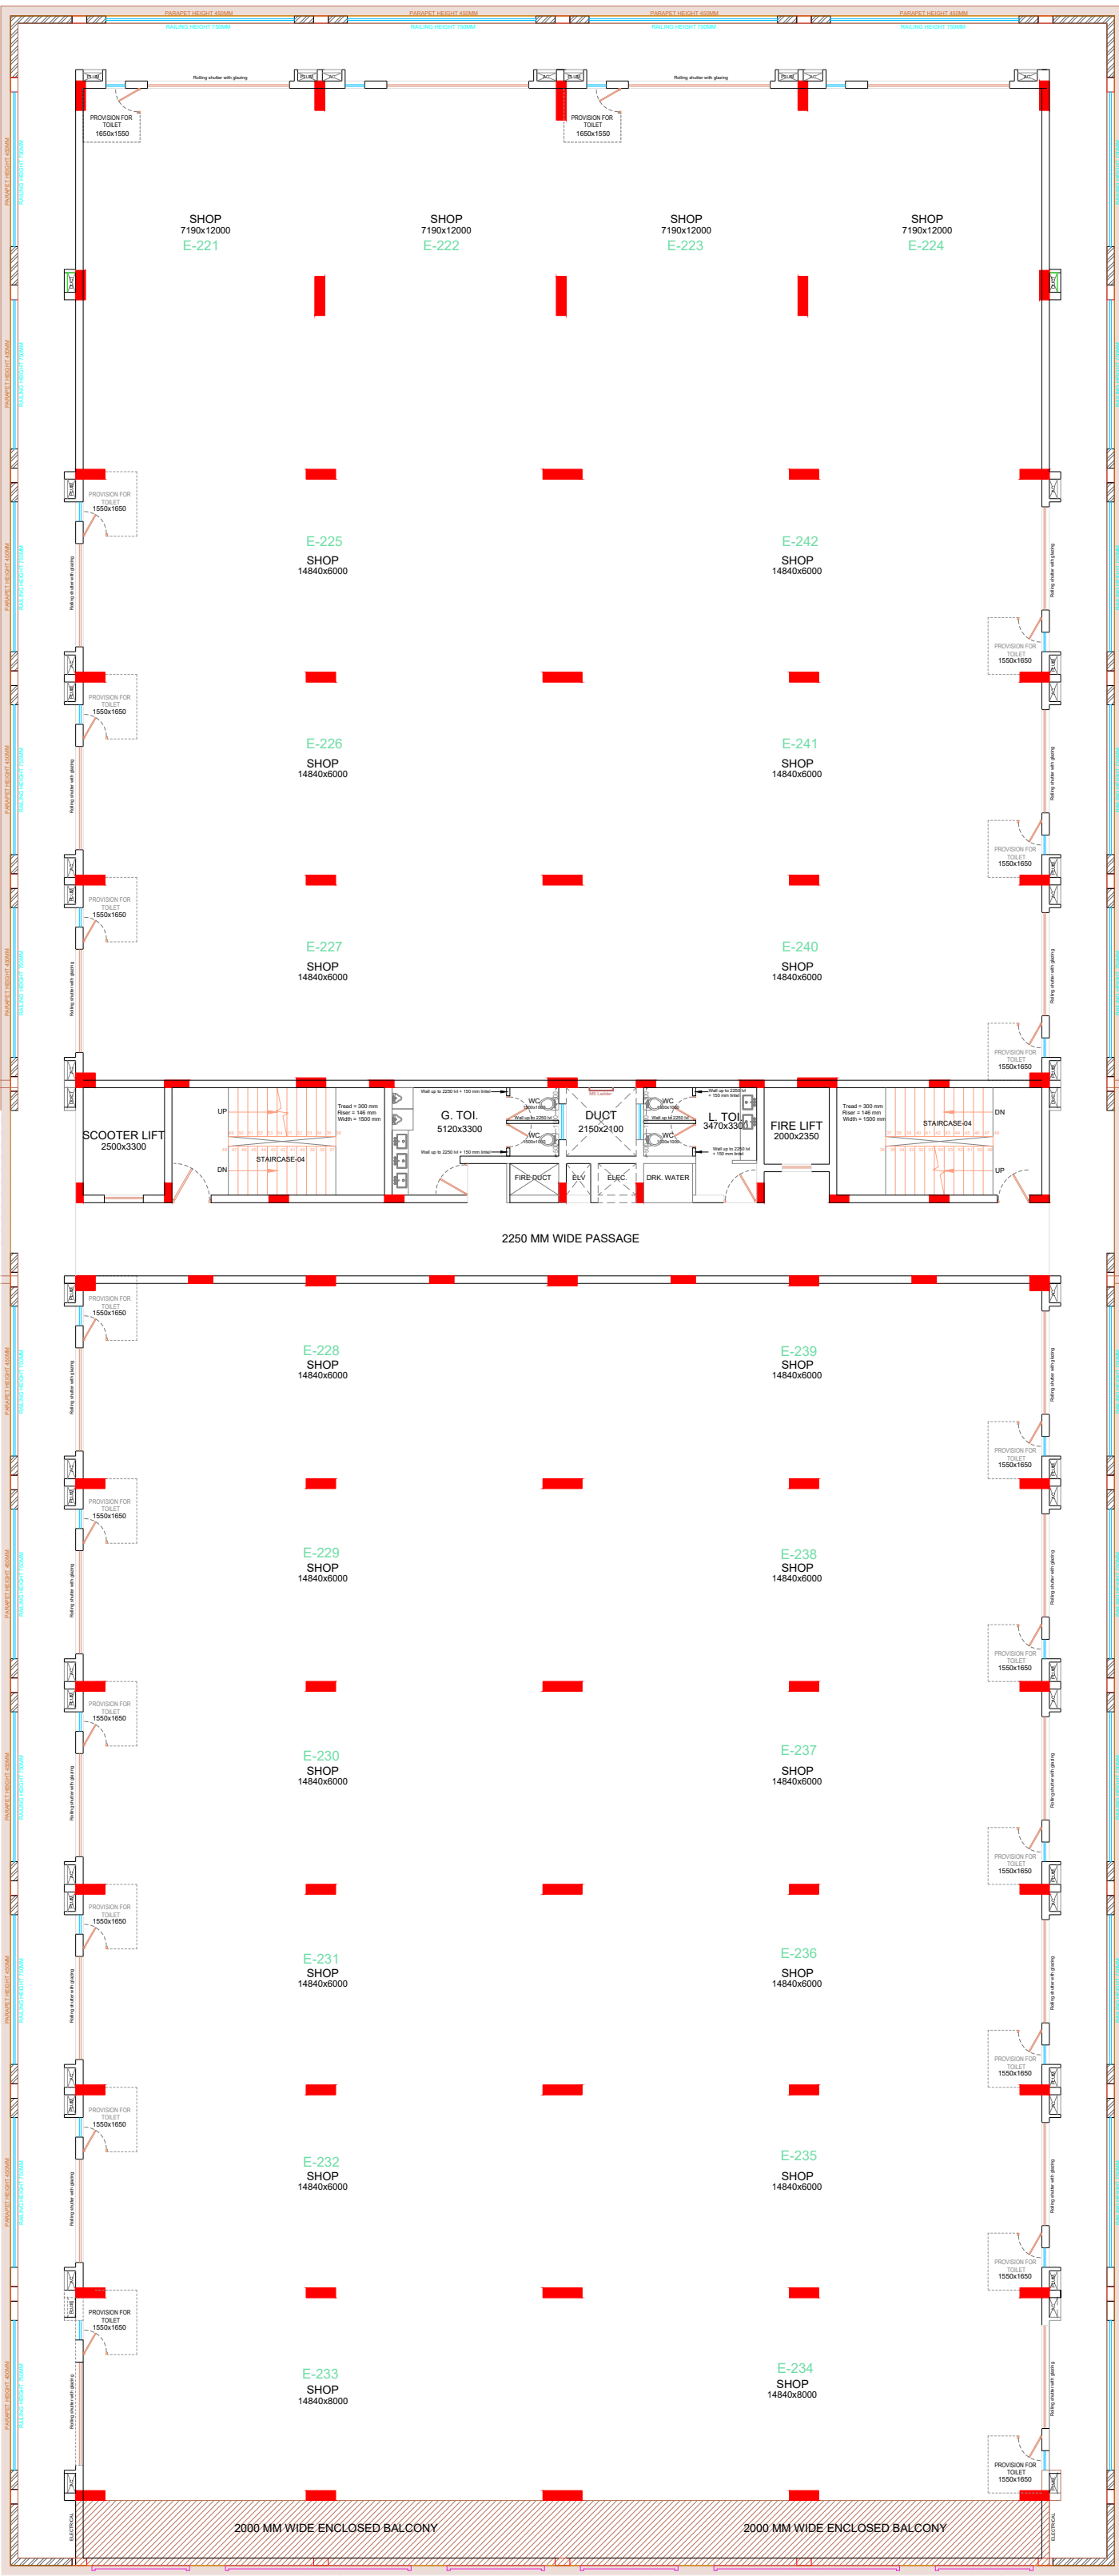

SECOND FLOOR
WING E

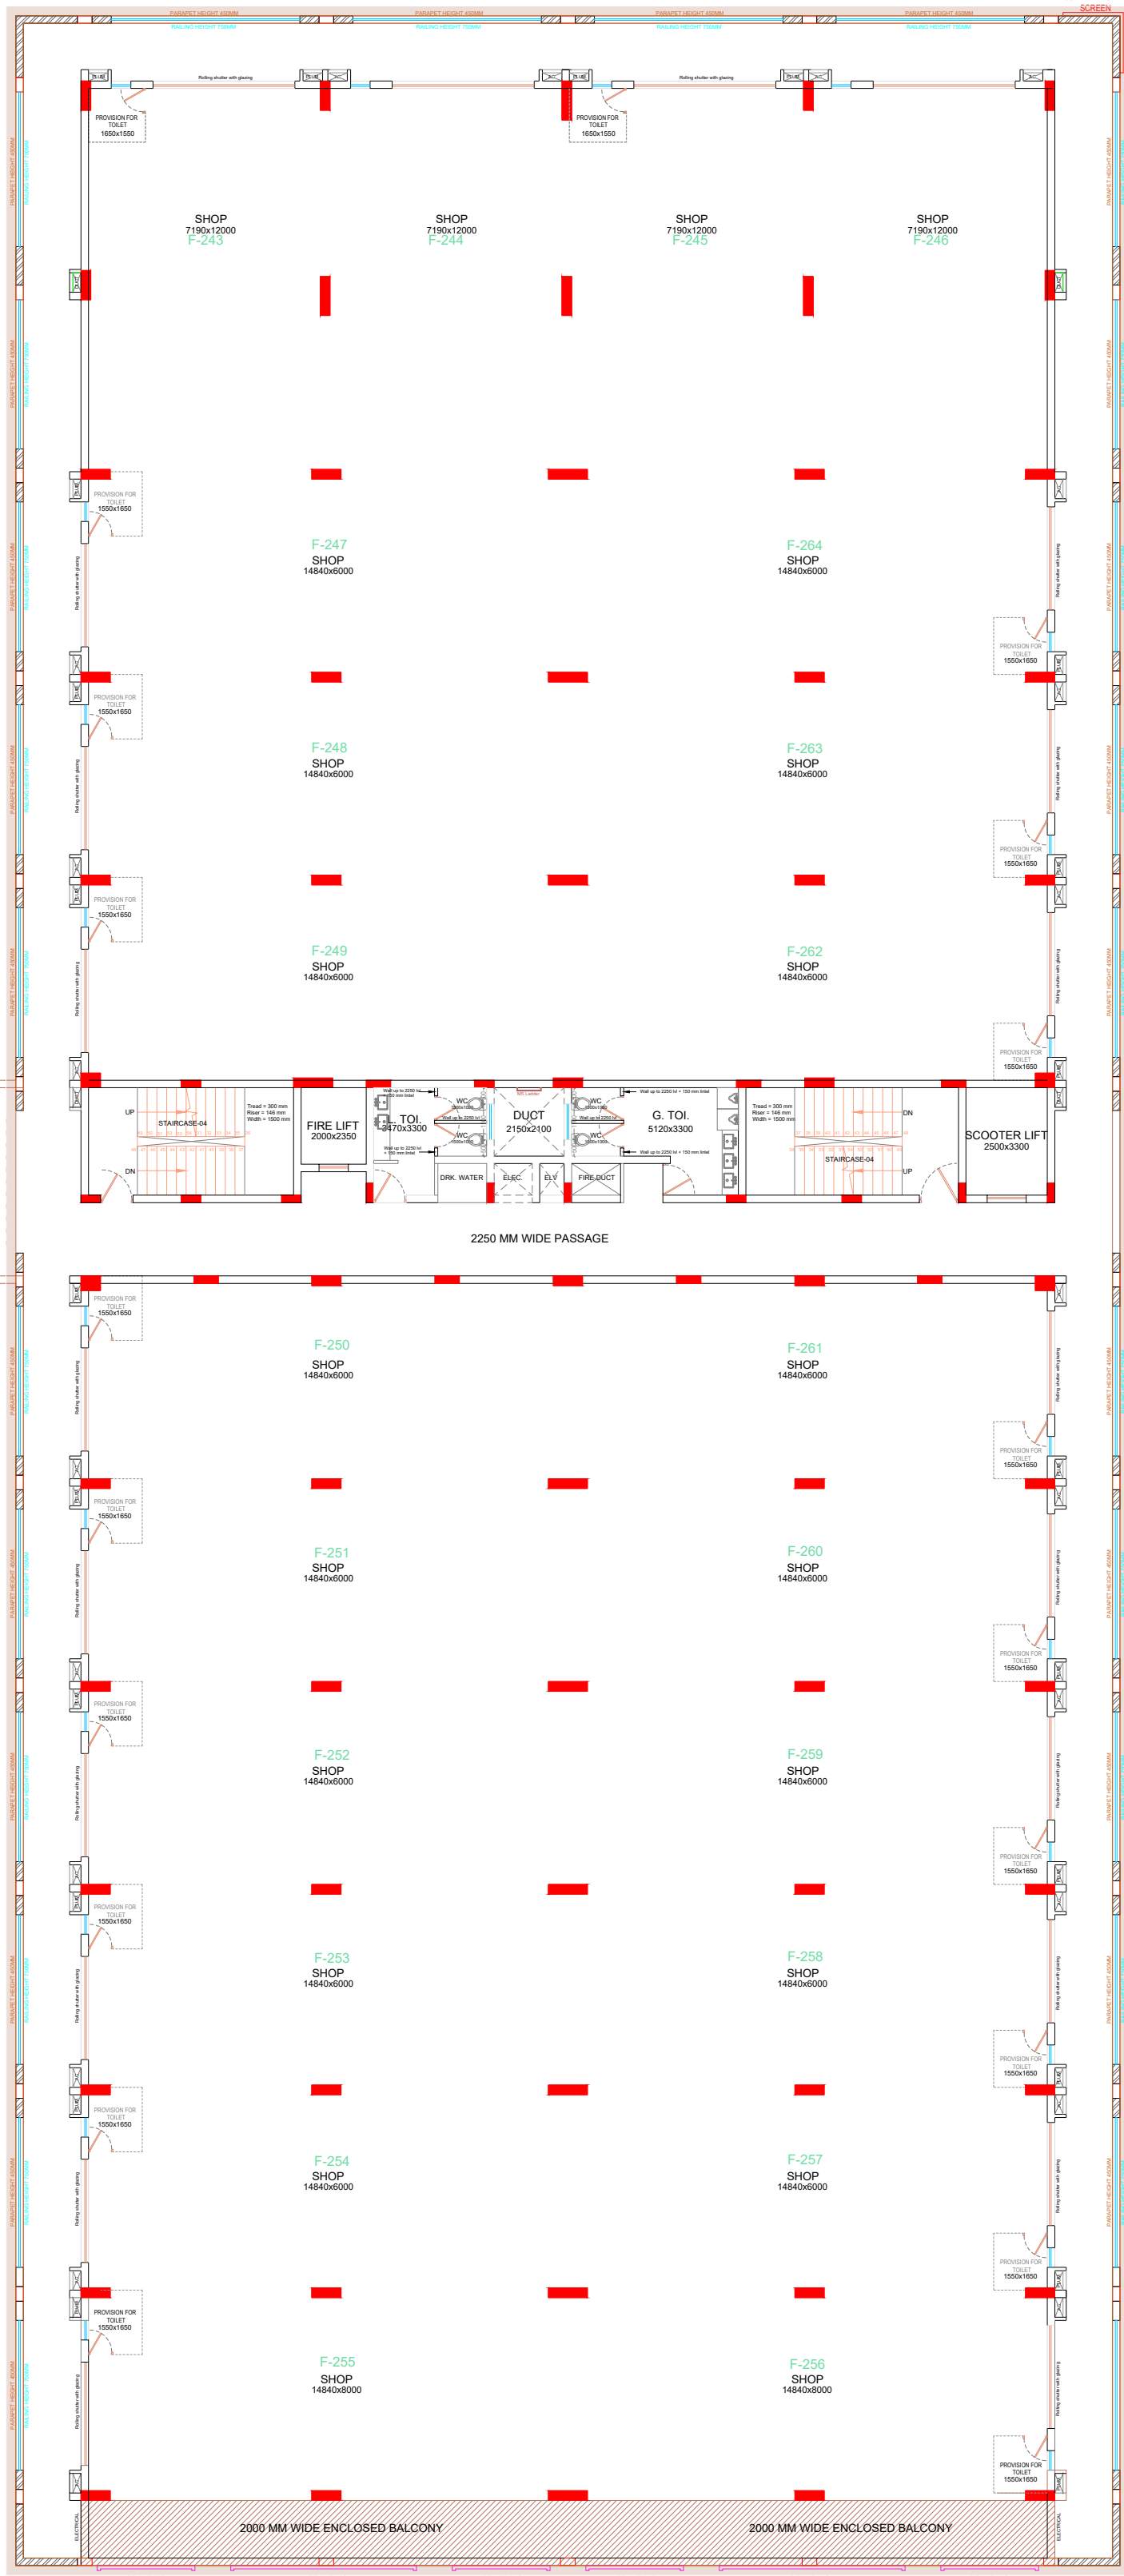

SECOND FLOOR
WING F

STAGE:
WORKING DRAWING

SHEET:
A1

PURPOSE:
ADVANCE COPY

COPYRIGHT:
THIS DRAWING IS A COPYRIGHT AND MUST NOT BE DISCLOSED, USED OR REPRODUCED IN ANY FORM WITHOUT THE EXPRESS PERMISSION FROM DISHA VISION.

- GENERAL NOTES:
- DO NOT SCALE THIS DRAWING.
 - ALL THE WRITTEN DIMENSIONS TO BE FOLLOWED.
 - ALL DIMENSIONS ARE IN MM UNLESS OTHERWISE SPECIFIED.
 - ALL THE DIMENSIONS ARE UNFINISHED UNLESS OTHERWISE SPECIFIED.
 - THE SIZES MENTIONED IN SCHEDULE FOR DOORS, WINDOWS & OPENINGS ARE CLEAR MASONRY OPENING SIZES.
 - ANY DISCREPANCY FOUND IN THIS DRAWING SHOULD BE BROUGHT TO THE NOTICE OF THE ARCHITECT BEFORE THE EXECUTION OF WORK.
 - THIS DRAWINGS SHALL BE REFERRED WITH DETAILS, STRUCTURAL, SERVICES AND OTHER RELEVANT DRAWINGS.
 - "DISHA VISION" SHALL NOT BE RESPONSIBLE IN ANY MANNER FOR THE CENTERING, SHUTTERING AND SCAFFOLDING ERECTED AT SITE FOR STRUCTURAL PURPOSE.
 - ALL THE LEVELS SPECIFIED ARE SFL (STRUCTURAL FINISH LEVEL) UNLESS OTHERWISE SPECIFIED.
 - ANY ADDITIONAL EXCAVATION / PROVISION REQUIRED FOR THE PURPOSE OF SOLING, WATERPROOFING, COMPACTION, RAFT SHALL BE AS PER THE DRAWING AND DETAILS GIVEN BY THE STRUCTURAL CONSULTANT & WATERPROOFING AGENCIES.

SCHEDULE FOR OPENINGS:

CONSULTANTS:

STRUCTURAL: PCPL, NAGPUR
ELECTRICAL: JHAVERI ASSOCIATES, AHMEDABAD
PLUMBING: JHAVERI ASSOCIATES, AHMEDABAD
FIRE FIGHTING: JHAVERI ASSOCIATES, AHMEDABAD
HVAC: ---
LANDSCAPE: ---

MASONRY DETAILS:

230/200 MM THICK WALL
100 MM THICK WALL
150 MM THICK WALL
LOW HEIGHT WALL


R8	---
R7	---
R6	---
R5	---
R4	---
R3	---
R2	---
R1	05-10-24 Brick work layout & door window schedule
R0	09-11-23 1st draft for structural co-ordination at site
REVISIONS:	

PROJECT:
KARAN KOTHARI BUSINESS PARK


TITLE:
PLOT 2 - SECOND FLOOR PLAN

SCALE:	1:175	NORTH:
DATE:		
DRAWN BY:		
CHECKED BY:	Akash M.	
DRAWING NO.:	---	

AKASH MOHOTA
+91 7276094577
akash.dishavision@outlook.com
www.dishavision.com
@dishavision
1st Floor, Monalisa Complex,
Opp. to Rajawade Police Station,
Amravati - 444601

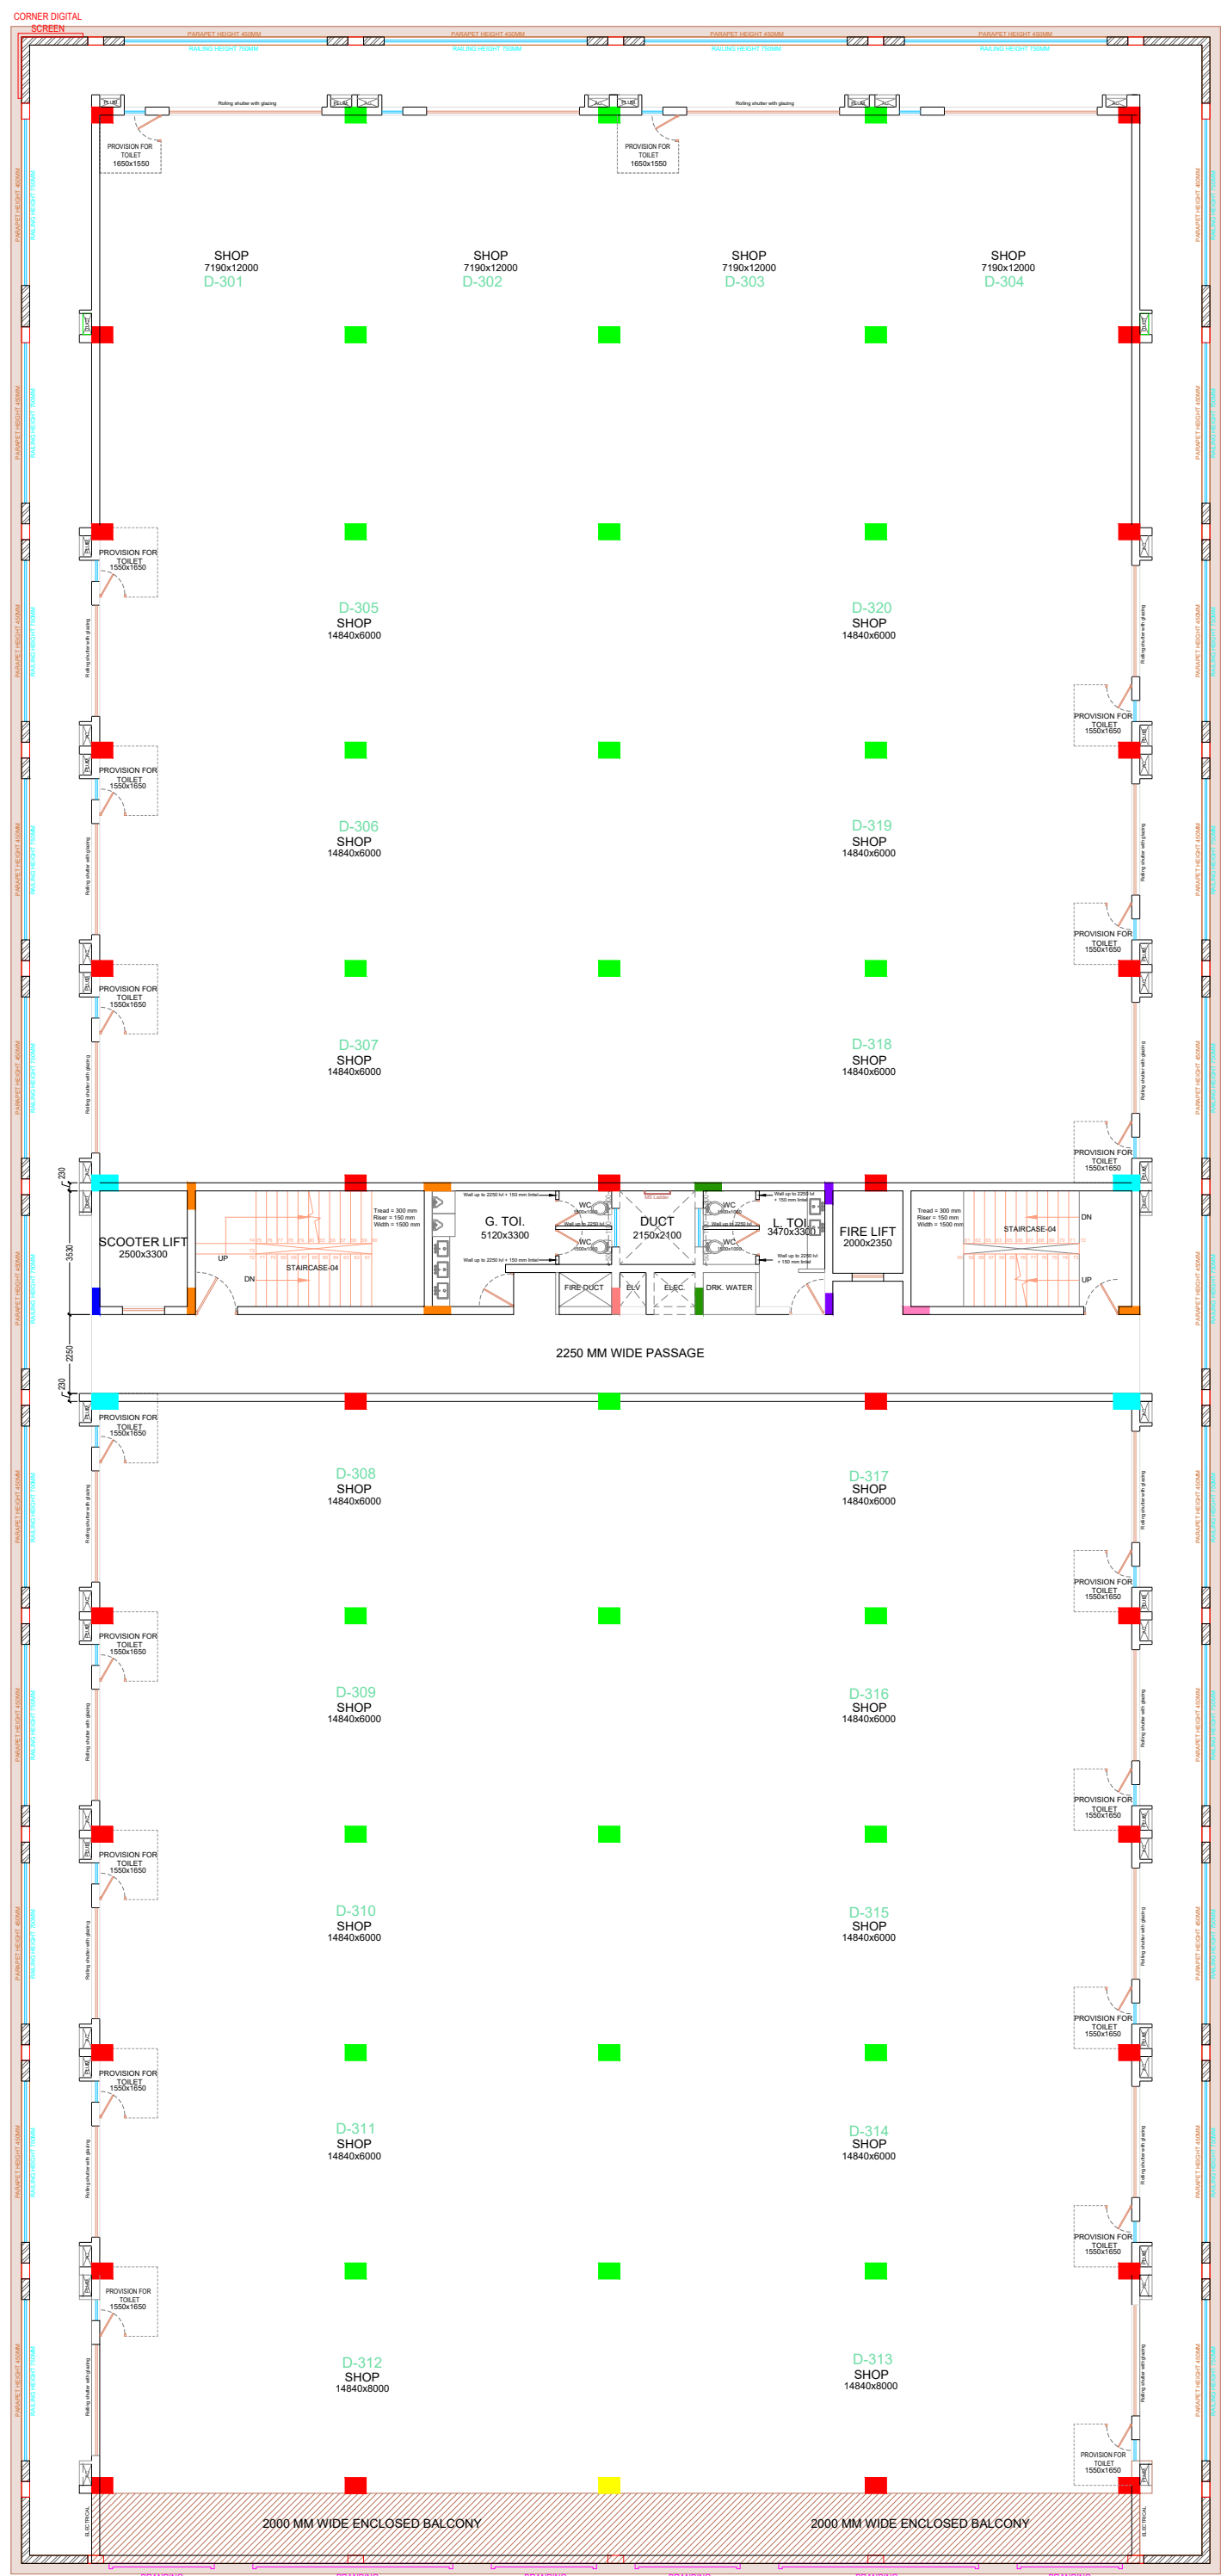

THIRD FLOOR
WING D

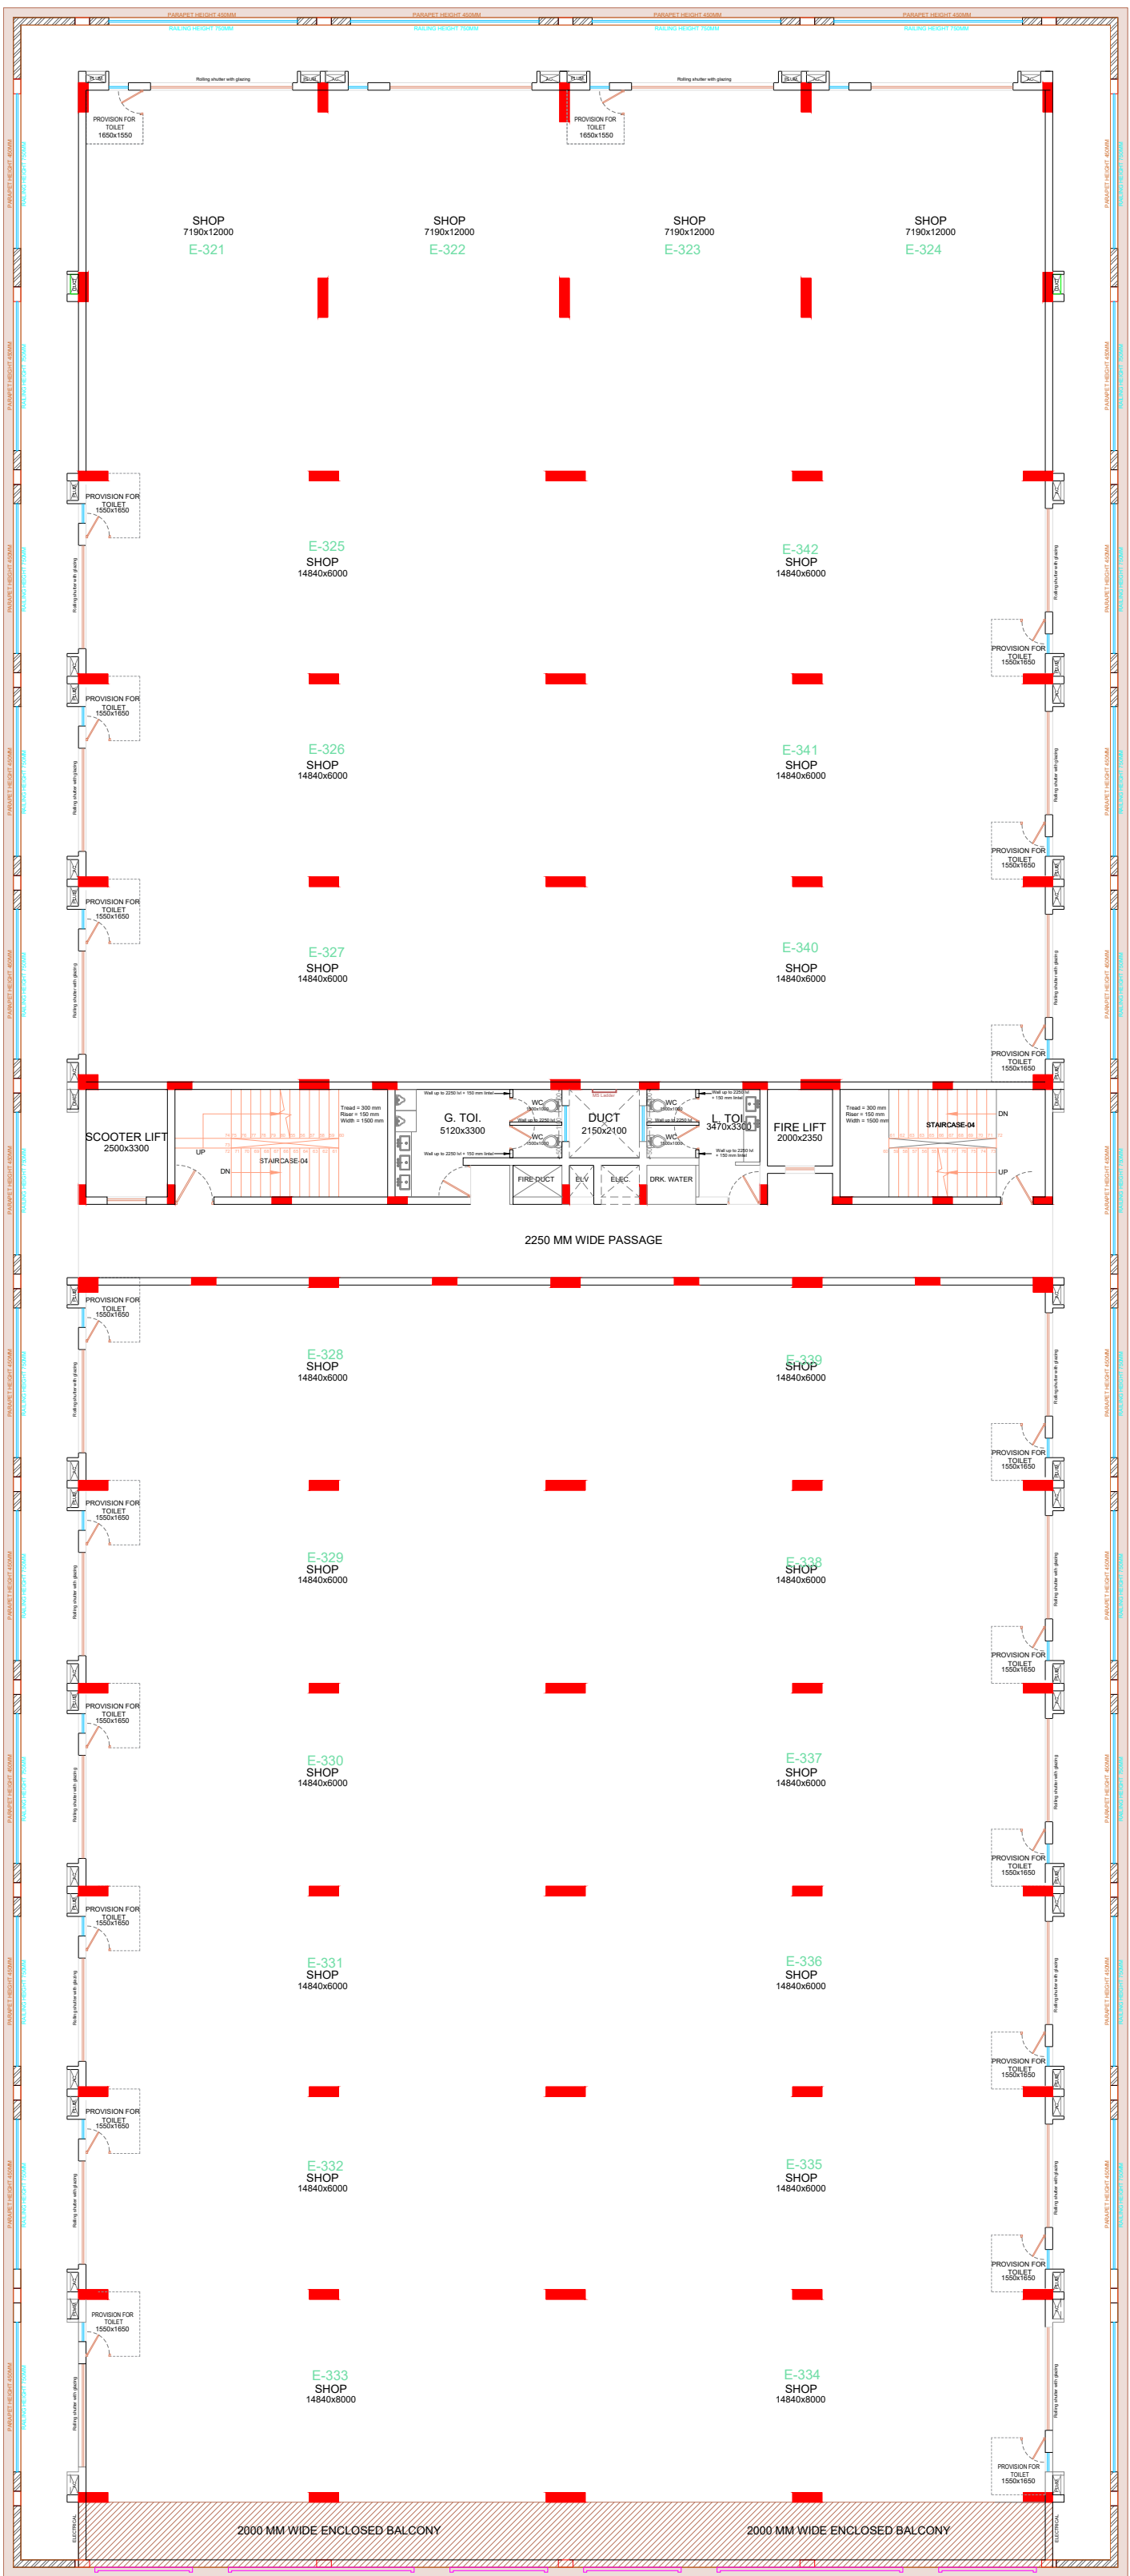

THIRD FLOOR
WING E

